

平面图 PLAN 1:4000 等高线 1 m（计曲线 5 m） N↑

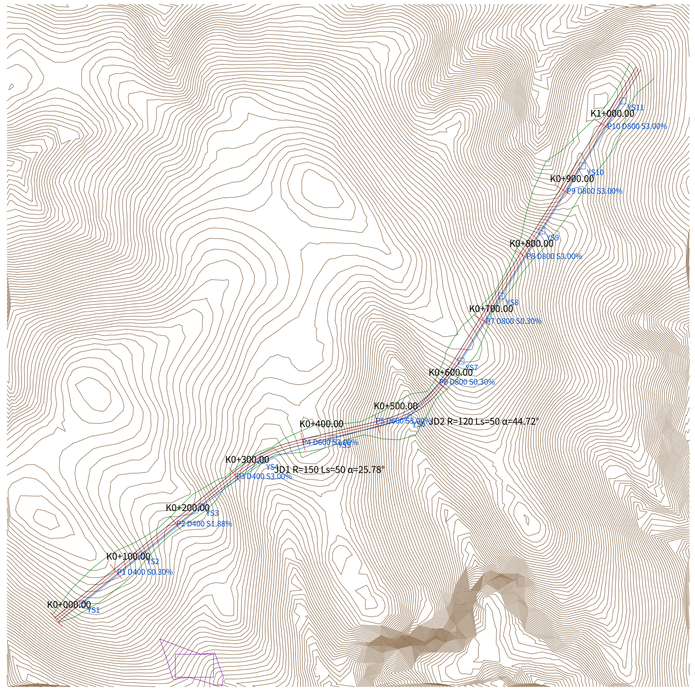

纵断面图 PROFILE H 1:1750 V 1:391（地面线棕色，设计线红色）

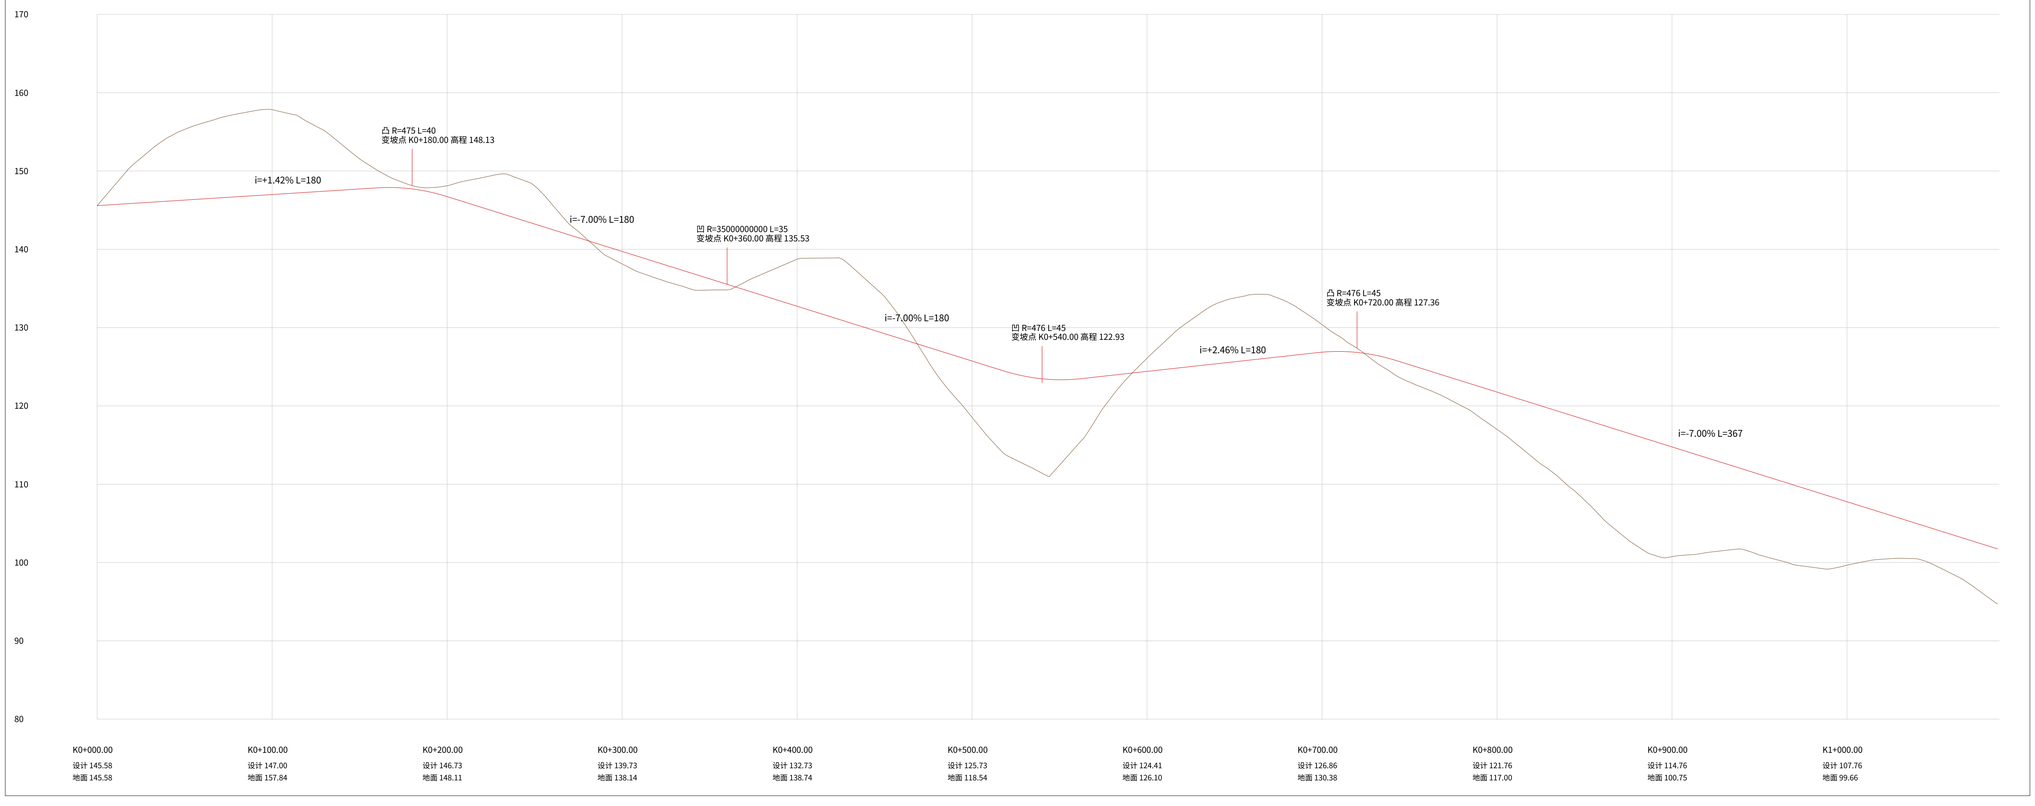

演示道路 Demo access road (USGS 3DEP, Palo Alto CA)

图名 Sheet: 平纵面图 Plan & Profile
图号 1/8
规范 Std: JtgD20_2017
设计速度 Design speed: 40 km/h
检查 Checks: 86/86 通过 pass
审计日志 Audit log head:
a521354394fc41ccd5fe36febd2c8e00
c7d988d7ed25f81bebf8ef16764be496
编制 Prepared by: civil-mcp agent tools
负责工程师 Engineer in responsible charge:
REVIEWER-PLACEHOLDER

初步设计 PRELIMINARY


不得用于施工

NOT FOR CONSTRUCTION

未经注册工程师审核盖章
Not reviewed or sealed by a licensed engineer.


注册工程师签章 ENGINEER SEAL / SIGNATURE

桩号 K0+000.00

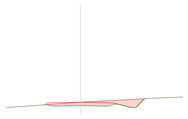


设计 145.58 地面 145.58 挖 6.8 m² 填 0.0 m²
横坡 左 -2.00% 右 -2.00% 坡脚/坡顶 左 6.4 右 4.6 m

桩号 K0+020.00

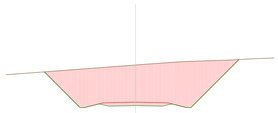


设计 145.86 地面 150.71 挖 107.7 m² 填 0.0 m²
横坡 左 -2.00% 右 -2.00% 坡脚/坡顶 左 13.5 右 11.9 m

桩号 K0+040.00

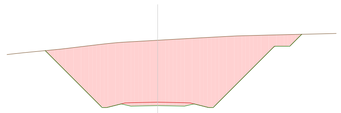

设计 146.14 地面 154.23 挖 201.7 m² 填 0.0 m²
横坡 左 -2.00% 右 -2.00% 坡脚/坡顶 左 18.8 右 14.7 m

桩号 K0+060.00

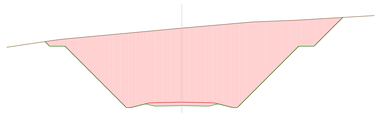

设计 146.43 地面 156.10 挖 263.0 m² 填 0.0 m²
横坡 左 -2.00% 右 -2.00% 坡脚/坡顶 左 21.0 右 17.9 m

桩号 K0+080.00

设计 146.71 地面 157.28 挖 299.4 m² 填 0.0 m²
横坡 左 -2.00% 右 -2.00% 坡脚/坡顶 左 22.5 右 18.2 m

桩号 K0+100.00

设计 147.00 地面 157.84 挖 305.2 m² 填 0.0 m²
横坡 左 -2.00% 右 -2.00% 坡脚/坡顶 左 22.3 右 18.5 m


桩号 K0+120.00

设计 147.28 地面 156.32 挖 238.4 m² 填 0.0 m²
横坡 左 -2.00% 右 -2.00% 坡脚/坡顶 左 19.8 右 17.6 m

桩号 K0+140.00


设计 147.56 地面 153.35 挖 131.1 m² 填 0.0 m²
横坡 左 -2.00% 右 -2.00% 坡脚/坡顶 左 14.2 右 12.9 m

桩号 K0+160.00

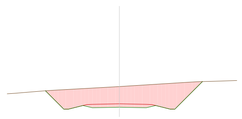


设计 147.85 地面 150.10 挖 49.0 m² 填 0.0 m²
横坡 左 -2.00% 右 -2.00% 坡脚/坡顶 左 10.9 右 9.7 m

桩号 K0+180.00

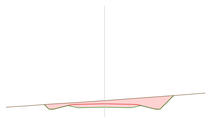


设计 147.71 地面 148.13 挖 14.8 m² 填 0.0 m²
横坡 左 -2.00% 右 -2.00% 坡脚/坡顶 左 9.0 右 7.9 m

桩号 K0+200.00

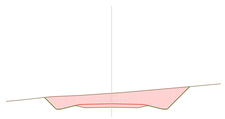

设计 146.73 地面 148.11 挖 32.6 m² 填 0.0 m²
横坡 左 -2.00% 右 -2.00% 坡脚/坡顶 左 10.2 右 8.8 m

桩号 K0+220.00

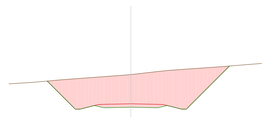

设计 145.33 地面 149.15 挖 85.1 m² 填 0.0 m²
横坡 左 -2.00% 右 -2.00% 坡脚/坡顶 左 12.9 右 10.9 m

演示道路 Demo access road (USGS 3DEP, Palo Alto CA)

图名 Sheet: 横断面图 Cross sections
图号 2/8
规范 Std: JtgD20_2017
设计速度 Design speed: 40 km/h
检查 Checks: 86/86 通过 pass
审计日志 Audit log head:
a521354394fc41ccd5fe36febd2c8e00
c7d988d7ed25f81bebf8ef16764be496
编制 Prepared by: civil-mcp agent tools
负责工程师 Engineer in responsible charge:
REVIEWER-PLACEHOLDER

初步设计 PRELIMINARY

不得用于施工


NOT FOR CONSTRUCTION

未经注册工程师审核盖章
Not reviewed or sealed by a licensed engineer.

注册工程师签章 ENGINEER SEAL / SIGNATURE


横断面图 CROSS SECTIONS 1:400（红=挖方 cut，绿=填方 fill，绿线=路基设计线 datum）

桩号 K0+240.00

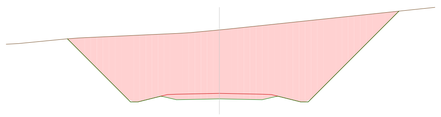


设计 143.93 地面 149.11 挖 121.3 m² 填 0.0 m²
横坡 左 -2.00% 右 -2.00% 坡脚/坡顶 左 14.7 右 12.4 m

桩号 K0+260.00

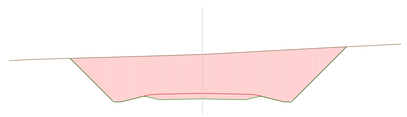


设计 142.53 地面 145.71 挖 69.7 m² 填 0.0 m²
横坡 左 -2.00% 右 -2.00% 坡脚/坡顶 左 11.8 右 10.8 m

桩号 K0+280.00

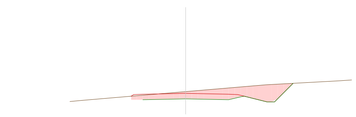


设计 141.13 地面 141.28 挖 9.8 m² 填 0.0 m²
横坡 左 -2.00% 右 -2.00% 坡脚/坡顶 左 8.8 右 4.5 m

桩号 K0+288.82

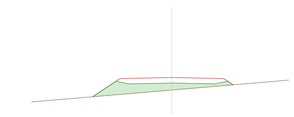


设计 140.51 地面 139.49 挖 0.0 m² 填 6.2 m²
横坡 左 -2.00% 右 -2.00% 坡脚/坡顶 左 5.0 右 6.5 m

桩号 K0+300.00

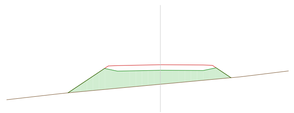


设计 139.73 地面 138.14 挖 0.0 m² 填 13.5 m²
横坡 左 -0.57% 右 -2.00% 坡脚/坡顶 左 5.8 右 7.5 m

桩号 K0+320.00

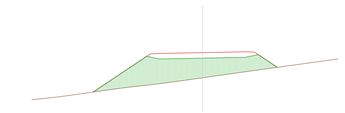


设计 138.33 地面 136.28 挖 0.0 m² 填 20.9 m²
横坡 左 +1.99% 右 -2.00% 坡脚/坡顶 左 6.1 右 8.9 m

桩号 K0+338.82

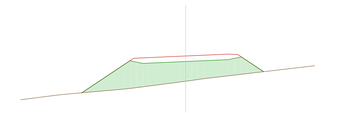


设计 137.01 地面 134.95 挖 0.0 m² 填 20.6 m²
横坡 左 +4.40% 右 -4.40% 坡脚/坡顶 左 6.4 右 8.5 m

桩号 K0+340.00

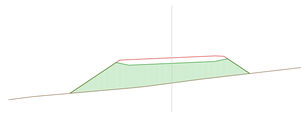


设计 136.93 地面 134.87 挖 0.0 m² 填 20.2 m²
横坡 左 +4.40% 右 -4.40% 坡脚/坡顶 左 6.4 右 8.3 m

桩号 K0+342.50

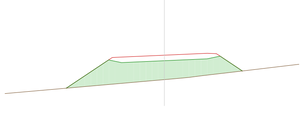


设计 136.76 地面 134.76 挖 0.0 m² 填 18.9 m²
横坡 左 +4.40% 右 -4.40% 坡脚/坡顶 左 6.4 右 8.0 m

桩号 K0+356.31

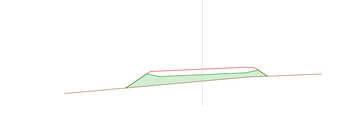


设计 135.79 地面 134.81 挖 0.0 m³ 填 6.1 m²
横坡 左 +4.40% 右 -4.40% 坡脚/坡顶 左 5.3 右 6.3 m

桩号 K0+360.00

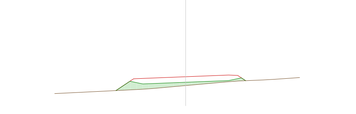

设计 135.53 地面 134.81 挖 0.0 m³ 填 3.1 m²
横坡 左 +3.93% 右 -3.93% 坡脚/坡顶 左 4.9 右 5.7 m

桩号 K0+377.50

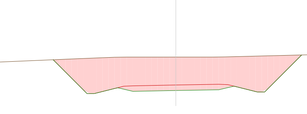

设计 134.31 地面 136.58 挖 47.7 m² 填 0.0 m³
横坡 左 +1.69% 右 -2.00% 坡脚/坡顶 左 10.3 右 10.0 m

演示道路 Demo access road (USGS 3DEP, Palo Alto CA)

图名 Sheet: 横断面图 Cross sections
图号 3/8
规范 Std: JtgD20_2017
设计速度 Design speed: 40 km/h
检查 Checks: 86/86 通过 pass
审计日志 Audit log head:
a521354394fc41ccd5fe36febd2c8e00
c7d988d7ed25f81bebf8ef16764be496
编制 Prepared by: civil-mcp agent tools
负责工程师 Engineer in responsible charge:
REVIEWER-PLACEHOLDER

初步设计 PRELIMINARY

不得用于施工

NOT FOR CONSTRUCTION

未经注册工程师审核盖章
Not reviewed or sealed by a licensed engineer.

注册工程师签章 ENGINEER SEAL / SIGNATURE


横断面图 CROSS SECTIONS 1:250（红=挖方 cut，绿=填方 fill，绿线=路基设计线 datum）

桩号 K0+380.00




设计 134.13 地面 136.82 挖 56.7 m² 填 0.0 m²
横坡 左 +1.37% 右 -2.00% 坡脚/坡顶 左 10.7 右 10.5 m

桩号 K0+400.00

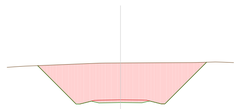


设计 132.73 地面 138.74 挖 136.8 m² 填 0.0 m²
横坡 左 -1.19% 右 -2.00% 坡脚/坡顶 左 14.1 右 13.5 m

桩号 K0+406.31

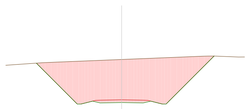


设计 132.29 地面 138.86 挖 155.5 m² 填 0.0 m²
横坡 左 -2.00% 右 -2.00% 坡脚/坡顶 左 15.1 右 13.9 m

桩号 K0+420.00

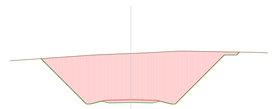


设计 131.33 地面 138.89 挖 184.0 m² 填 0.0 m²
横坡 左 -2.00% 右 -2.00% 坡脚/坡顶 左 17.7 右 14.7 m

桩号 K0+440.00

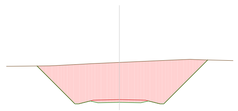


设计 129.93 地面 136.00 挖 140.4 m² 填 0.0 m²
横坡 左 -2.00% 右 -2.00% 坡脚/坡顶 左 14.4 右 13.4 m

桩号 K0+460.00

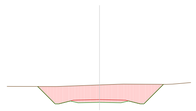


设计 128.53 地面 130.93 挖 50.5 m³ 填 0.0 m²
横坡 左 -2.00% 右 -2.00% 坡脚/坡顶 左 10.4 右 10.1 m

桩号 K0+480.00

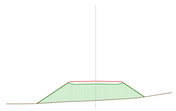


设计 127.13 地面 123.95 挖 0.0 m³ 填 36.6 m³
横坡 左 -2.00% 右 -2.00% 坡脚/坡顶 左 8.0 右 9.6 m

桩号 K0+488.04

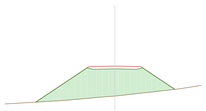


设计 126.57 地面 121.68 挖 0.0 m³ 填 71.7 m³
横坡 左 -2.00% 右 -2.00% 坡脚/坡顶 左 9.8 右 12.9 m

桩号 K0+500.00

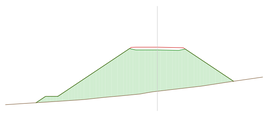


设计 125.73 地面 118.54 挖 0.0 m³ 填 139.0 m³
横坡 左 -2.00% 右 +0.03% 坡脚/坡顶 左 12.4 右 19.8 m

桩号 K0+517.50

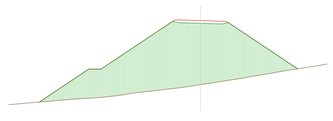


设计 124.51 地面 114.05 挖 0.0 m³ 填 263.9 m³
横坡 左 -3.01% 右 +3.01% 坡脚/坡顶 左 15.9 右 26.3 m

桩号 K0+520.00

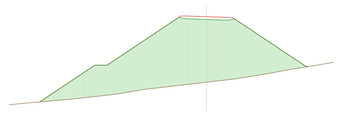

设计 124.34 地面 113.65 挖 0.0 m³ 填 277.7 m³
横坡 左 -3.43% 右 +3.43% 坡脚/坡顶 左 16.5 右 27.3 m

桩号 K0+538.04

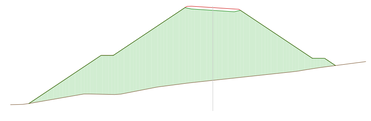

设计 123.51 地面 111.64 挖 0.0 m³ 填 340.3 m²
横坡 左 -6.50% 右 +6.50% 坡脚/坡顶 左 20.0 右 30.0 m

演示道路 Demo access road (USGS 3DEP, Palo Alto CA)

图名 Sheet: 横断面图 Cross sections

图号 4/8

规范 Std: JtgD20_2017

设计速度 Design speed: 40 km/h

检查 Checks: 86/86 通过 pass

审计日志 Audit log head:

a521354394fc41ccd5fe36febd2c8e00

c7d988d7ed25f81bebf8ef16764be496

编制 Prepared by: civil-mcp agent tools

负责工程师 Engineer in responsible charge:

REVIEWER-PLACEHOLDER

初步设计 PRELIMINARY

不得用于施工

NOT FOR CONSTRUCTION


未经注册工程师审核盖章

Not reviewed or sealed by a licensed engineer.

注册工程师签章 ENGINEER SEAL / SIGNATURE


横断面图 CROSS SECTIONS 1:500（红=挖方 cut，绿=填方 fill，绿线=路基设计线 datum）

桩号 K0+540.00

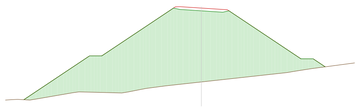


设计 123.46 地面 111.40 挖 0.0 m² 填 340.8 m²
横坡 左 -6.50% 右 +6.50% 坡脚/坡顶 左 20.2 右 29.0 m

桩号 K0+560.00

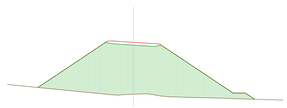

设计 123.43 地面 114.96 挖 0.0 m² 填 177.2 m²
横坡 左 -6.50% 右 +6.50% 坡脚/坡顶 左 19.8 右 15.6 m

桩号 K0+562.50

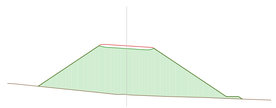

设计 123.49 地面 115.50 挖 0.0 m² 填 154.1 m²
横坡 左 -6.50% 右 +6.50% 坡脚/坡顶 左 18.9 右 14.4 m

桩号 K0+580.00



设计 123.92 地面 121.23 挖 0.0 m² 填 29.7 m²
横坡 左 -6.50% 右 +6.50% 坡脚/坡顶 左 8.8 右 7.7 m

桩号 K0+581.69

设计 123.96 地面 121.72 挖 0.0 m² 填 22.5 m²
横坡 左 -6.50% 右 +6.50% 坡脚/坡顶 左 8.0 右 7.2 m

桩号 K0+600.00

设计 124.41 地面 126.10 挖 35.7 m² 填 0.0 m²
横坡 左 -3.39% 右 +3.39% 坡脚/坡顶 左 9.4 右 9.6 m


桩号 K0+620.00

设计 124.90 地面 130.16 挖 116.4 m² 填 0.0 m²
横坡 左 -2.00% 右 -0.01% 坡脚/坡顶 左 13.1 右 13.0 m

桩号 K0+631.69


设计 125.19 地面 132.03 挖 161.8 m² 填 0.0 m²
横坡 左 -2.00% 右 -2.00% 坡脚/坡顶 左 14.8 右 14.5 m

桩号 K0+640.00

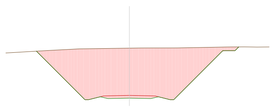


设计 125.39 地面 133.11 挖 189.1 m² 填 0.0 m²
横坡 左 -2.00% 右 -2.00% 坡脚/坡顶 左 17.9 右 15.2 m

桩号 K0+660.00

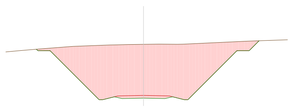


设计 125.89 地面 134.22 挖 212.2 m² 填 0.0 m²
横坡 左 -2.00% 右 -2.00% 坡脚/坡顶 左 18.9 右 17.5 m

桩号 K0+680.00

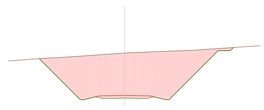

设计 126.38 地面 133.29 挖 164.0 m² 填 0.0 m²
横坡 左 -2.00% 右 -2.00% 坡脚/坡顶 左 17.8 右 13.9 m

桩号 K0+697.50

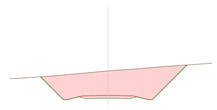

设计 126.81 地面 130.80 挖 86.8 m² 填 0.0 m²
横坡 左 -2.00% 右 -2.00% 坡脚/坡顶 左 12.9 右 11.0 m

横断面图 CROSS SECTIONS 1:500（红=挖方 cut，绿=填方 fill，绿线=路基设计线 datum）

演示道路 Demo access road (USGS 3DEP, Palo Alto CA)

图名 Sheet: 横断面图 Cross sections

图号 5/8

规范 Std: JtgD20_2017

设计速度 Design speed: 40 km/h

检查 Checks: 86/86 通过 pass

审计日志 Audit log head:

a521354394fc41ccd5fe36febd2c8e00

c7d988d7ed25f81bebf8ef16764be496

编制 Prepared by: civil-mcp agent tools

负责工程师 Engineer in responsible charge:

REVIEWER-PLACEHOLDER

初步设计 PRELIMINARY

不得用于施工


NOT FOR CONSTRUCTION

未经注册工程师审核盖章

Not reviewed or sealed by a licensed engineer.


注册工程师签章 ENGINEER SEAL / SIGNATURE

桩号 K0+700.00

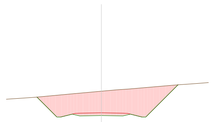


设计 126.86 地面 130.38 挖 76.3 m² 填 0.0 m²
横坡 左 -2.00% 右 -2.00% 坡脚/坡顶 左 12.5 右 10.5 m

桩号 K0+720.00

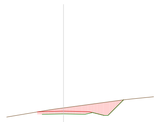


设计 126.83 地面 127.36 挖 16.7 m² 填 0.0 m²
横坡 左 -2.00% 右 -2.00% 坡脚/坡顶 左 9.8 右 4.3 m

桩号 K0+740.00

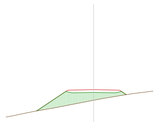


设计 125.96 地面 124.22 挖 0.0 m² 填 17.5 m²
横坡 左 -2.00% 右 -2.00% 坡脚/坡顶 左 5.3 右 9.3 m

桩号 K0+742.50

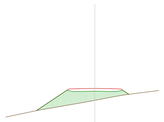


设计 125.79 地面 123.84 挖 0.0 m² 填 19.9 m²
横坡 左 -2.00% 右 -2.00% 坡脚/坡顶 左 5.5 右 9.5 m

桩号 K0+760.00

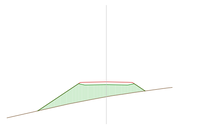


设计 124.56 地面 122.12 挖 0.0 m² 填 29.4 m²
横坡 左 -2.00% 右 -2.00% 坡脚/坡顶 左 6.3 右 11.2 m

桩号 K0+780.00

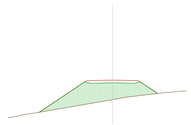


设计 123.16 地面 119.97 挖 0.0 m² 填 41.6 m²
横坡 左 -2.00% 右 -2.00% 坡脚/坡顶 左 7.4 右 12.0 m

桩号 K0+800.00

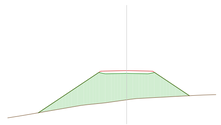


设计 121.76 地面 117.00 挖 0.0 m² 填 75.6 m²
横坡 左 -2.00% 右 -2.00% 坡脚/坡顶 左 10.2 右 14.4 m

桩号 K0+820.00

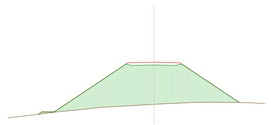


设计 120.36 地面 113.49 挖 0.0 m² 填 127.9 m²
横坡 左 -2.00% 右 -2.00% 坡脚/坡顶 左 14.0 右 18.9 m

桩号 K0+840.00

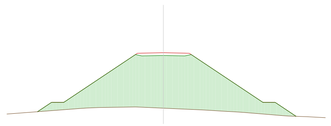


设计 118.96 地面 109.91 挖 0.0 m² 填 209.0 m²
横坡 左 -2.00% 右 -2.00% 坡脚/坡顶 左 21.7 右 20.5 m

桩号 K0+860.00

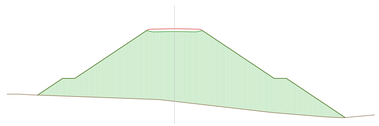


设计 117.56 地面 105.71 挖 0.0 m³ 填 341.5 m³
横坡 左 -2.00% 右 -2.00% 坡脚/坡顶 左 27.9 右 22.3 m

桩号 K0+880.00

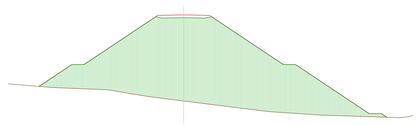

设计 116.16 地面 102.10 挖 0.0 m³ 填 439.8 m³
横坡 左 -2.00% 右 -2.00% 坡脚/坡顶 左 33.2 右 23.6 m

桩号 K0+900.00

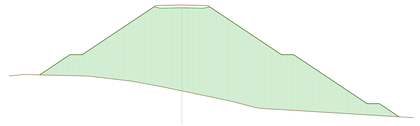

设计 114.76 地面 100.75 挖 0.0 m² 填 463.4 m²
横坡 左 -2.00% 右 -2.00% 坡脚/坡顶 左 35.5 右 23.2 m

演示道路 Demo access road (USGS 3DEP, Palo Alto CA)

图名 Sheet: 横断面图 Cross sections
图号 6/8
规范 Std: JtgD20_2017
设计速度 Design speed: 40 km/h
检查 Checks: 86/86 通过 pass
审计日志 Audit log head:
a521354394fc41ccd5fe36febd2c8e00
c7d988d7ed25f81bebf8ef16764be496
编制 Prepared by: civil-mcp agent tools
负责工程师 Engineer in responsible charge:
REVIEWER-PLACEHOLDER

初步设计 PRELIMINARY

不得用于施工

NOT FOR CONSTRUCTION

未经注册工程师审核盖章
Not reviewed or sealed by a licensed engineer.

注册工程师签章 ENGINEER SEAL / SIGNATURE

横断面图 CROSS SECTIONS 1:500（红=挖方 cut，绿=填方 fill，绿线=路基设计线 datum）

桩号 K0+920.00




设计 113.36 地面 101.28 挖 0.0 m² 填 405.9 m²
横坡 左 -2.00% 右 -2.00% 坡脚/坡顶 左 16.6 右 22.6 m

桩号 K0+940.00




设计 111.96 地面 101.71 挖 0.0 m² 填 305.0 m²
横坡 左 -2.00% 右 -2.00% 坡脚/坡顶 左 29.4 右 24.2 m

桩号 K0+960.00

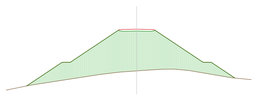


设计 110.56 地面 100.35 挖 0.0 m² 填 282.0 m²
横坡 左 -2.00% 右 -2.00% 坡脚/坡顶 左 24.0 右 26.9 m

桩号 K0+980.00

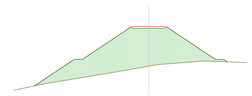


设计 109.16 地面 99.40 挖 0.0 m² 填 258.0 m²
横坡 左 -2.00% 右 -2.00% 坡脚/坡顶 左 19.2 右 28.0 m

桩号 K1+000.00

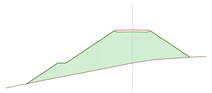


设计 107.76 地面 99.66 挖 0.0 m² 填 193.1 m²
横坡 左 -2.00% 右 -2.00% 坡脚/坡顶 左 14.1 右 25.9 m

桩号 K1+020.00

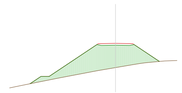


设计 106.36 地面 100.42 挖 0.0 m² 填 111.0 m²
横坡 左 -2.00% 右 -2.00% 坡脚/坡顶 左 10.7 右 20.9 m

桩号 K1+040.00

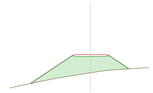


设计 104.96 地面 100.48 挖 0.0 m² 填 69.7 m²
横坡 左 -2.00% 右 -2.00% 坡脚/坡顶 左 9.4 右 14.8 m

桩号 K1+060.00

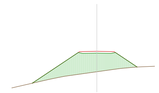


设计 103.56 地面 98.56 挖 0.0 m² 填 81.0 m²
横坡 左 -2.00% 右 -2.00% 坡脚/坡顶 左 9.9 右 15.8 m

桩号 K1+080.00

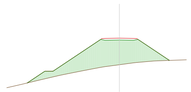

设计 102.16 地面 95.65 挖 0.0 m² 填 131.3 m²
横坡 左 -2.00% 右 -2.00% 坡脚/坡顶 左 12.3 右 22.6 m

桩号 K1+087.02

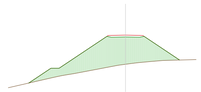

设计 101.67 地面 94.53 挖 0.0 m² 填 154.8 m²
横坡 左 -2.00% 右 -2.00% 坡脚/坡顶 左 13.2 右 23.7 m

演示道路 Demo access road (USGS 3DEP, Palo Alto CA)

图名 Sheet: 横断面图 Cross sections
图号 7/8
规范 Std: JtgD20_2017
设计速度 Design speed: 40 km/h
检查 Checks: 86/86 通过 pass
审计日志 Audit log head:
a521354394fc41ccd5fe36febd2c8e00
c7d988d7ed25f81bebf8ef16764be496
编制 Prepared by: civil-mcp agent tools
负责工程师 Engineer in responsible charge:
REVIEWER-PLACEHOLDER

初步设计 PRELIMINARY

不得用于施工


NOT FOR CONSTRUCTION

未经注册工程师审核盖章
Not reviewed or sealed by a licensed engineer.

注册工程师签章 ENGINEER SEAL / SIGNATURE

横断面图 CROSS SECTIONS 1:750（红=挖方 cut，绿=填方 fill，绿线=路基设计线 datum）

土方调配图 MASS HAUL (m³) 挖方系数 cut factor 0.90 终点累计 -32912 m³

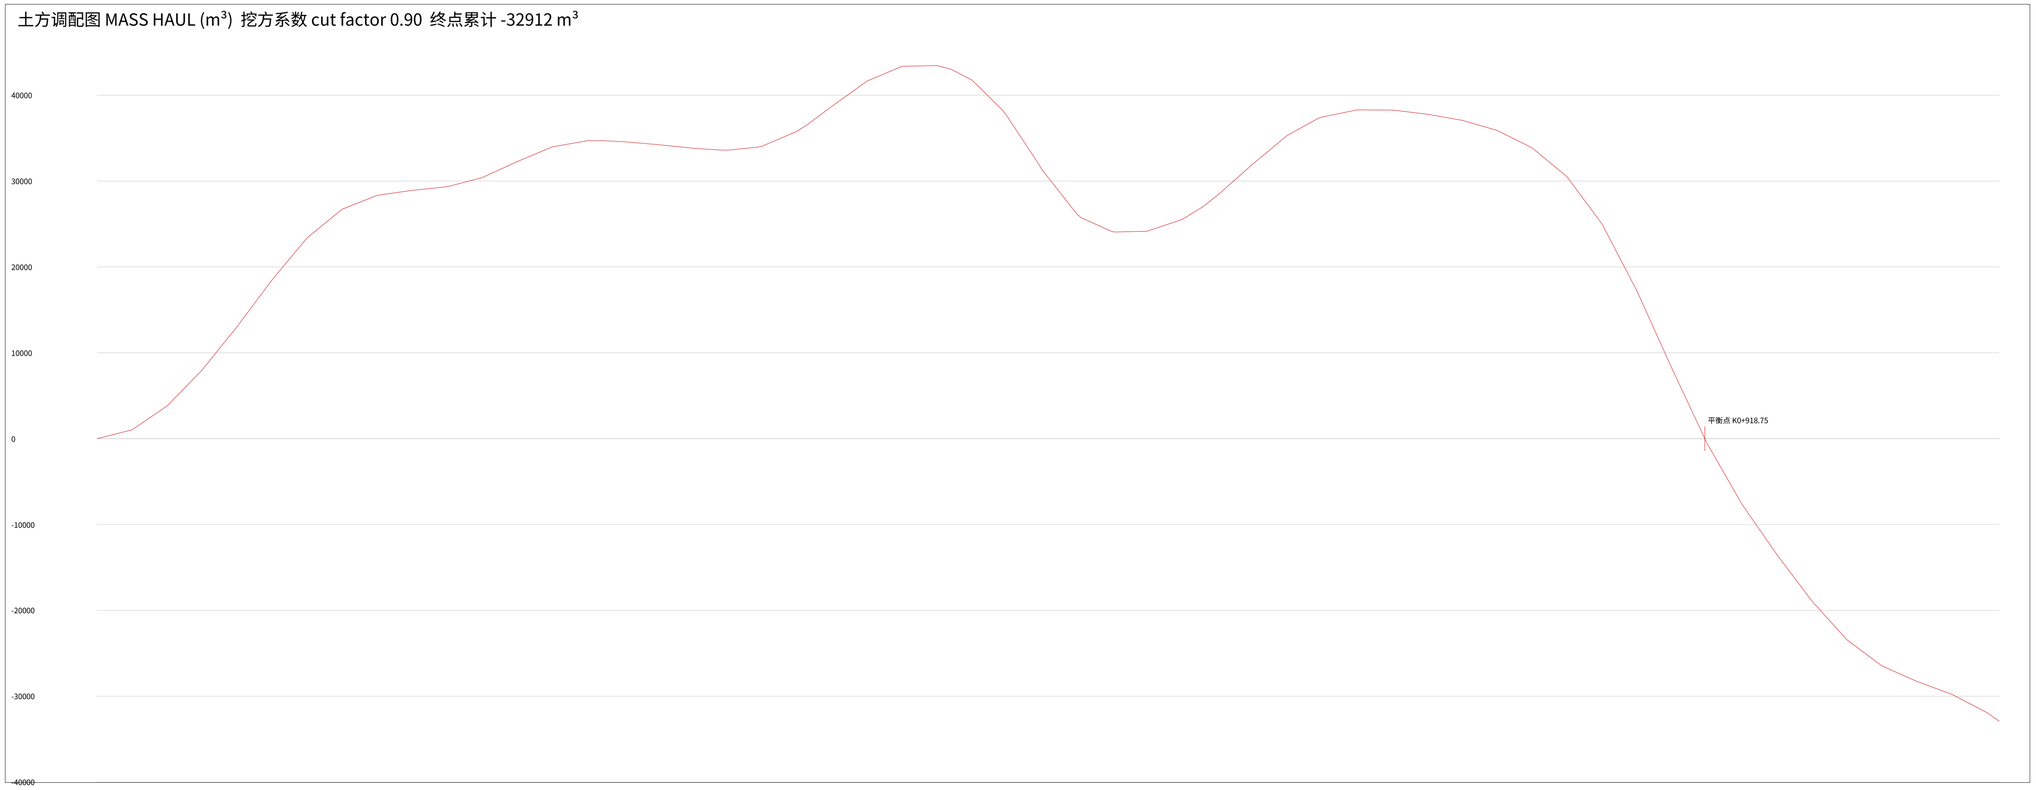

桩号范围 Station	挖方 Cut m³	填方 Fill m³	沥青面层 AC m³	水稳基层 Base m³	底基层 Subbase m³
K0+000.00–K0+100.00	20557	0	35.0	140.0	140.0
K0+100.00–K0+200.00	12044	0	35.0	140.0	140.0
K0+200.00–K0+300.00	5991	137	35.0	140.0	140.0
K0+300.00–K0+400.00	2482	1024	35.0	140.0	140.0
K0+400.00–K0+500.00	8904	2062	35.0	140.0	140.0
K0+500.00–K0+600.00	327	17897	35.0	140.0	140.0
K0+600.00–K0+700.00	14778	0	35.0	140.0	140.0
K0+700.00–K0+800.00	1097	2535	35.0	140.0	140.0
K0+800.00–K0+900.00	0	27755	35.0	140.0	140.0
K0+900.00–K1+000.00	0	31583	35.0	140.0	140.0
K1+000.00–K1+100.00	0	9480	30.5	121.8	121.8
合计 Total	66180	92474	380.5	1521.8	1521.8

管道材料表 Pipe schedule

钢筋混凝土管 RCP DN400: 299.0 m
钢筋混凝土管 RCP DN600: 199.2 m
钢筋混凝土管 RCP DN800: 501.2 m
检查井 Structures: 11

场平 Grading yard: 挖 2475 m³ 填 2242 m³ (方格网 0.25 m)

演示道路 Demo access road (USGS 3DEP, Palo Alto CA)

图名 Sheet: 土方调配及工程量 Mass haul & quantities
图号 8/8
规范 Std: JtgD20_2017
设计速度 Design speed: 40 km/h
检查 Checks: 86/86 通过 pass
审计日志 Audit log head:
a521354394fc41ccd5fe36febd2c8e00
c7d988d7ed25f81bebf8ef16764be496
编制 Prepared by: civil-mcp agent tools
负责工程师 Engineer in responsible charge:
REVIEWER-PLACEHOLDER

初步设计 PRELIMINARY

不得用于施工

NOT FOR CONSTRUCTION

未经注册工程师审核盖章
Not reviewed or sealed by a licensed engineer.

注册工程师签章 ENGINEER SEAL / SIGNATURE