

PLAN 1:5000 contours 1 m (major 5 m) N up

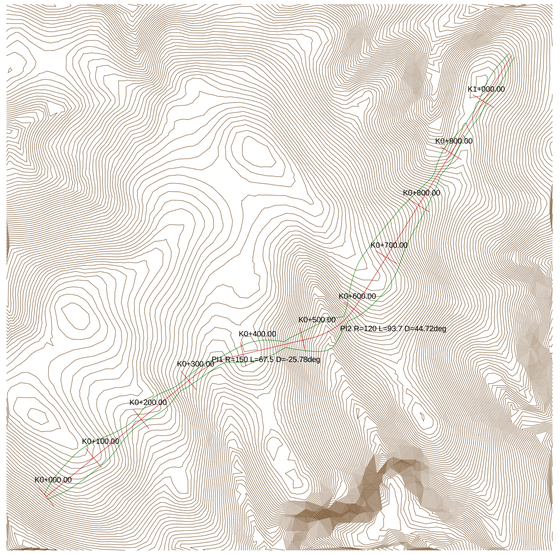

PROFILE H 1:1727 V 1:375 (ground brown, design red)

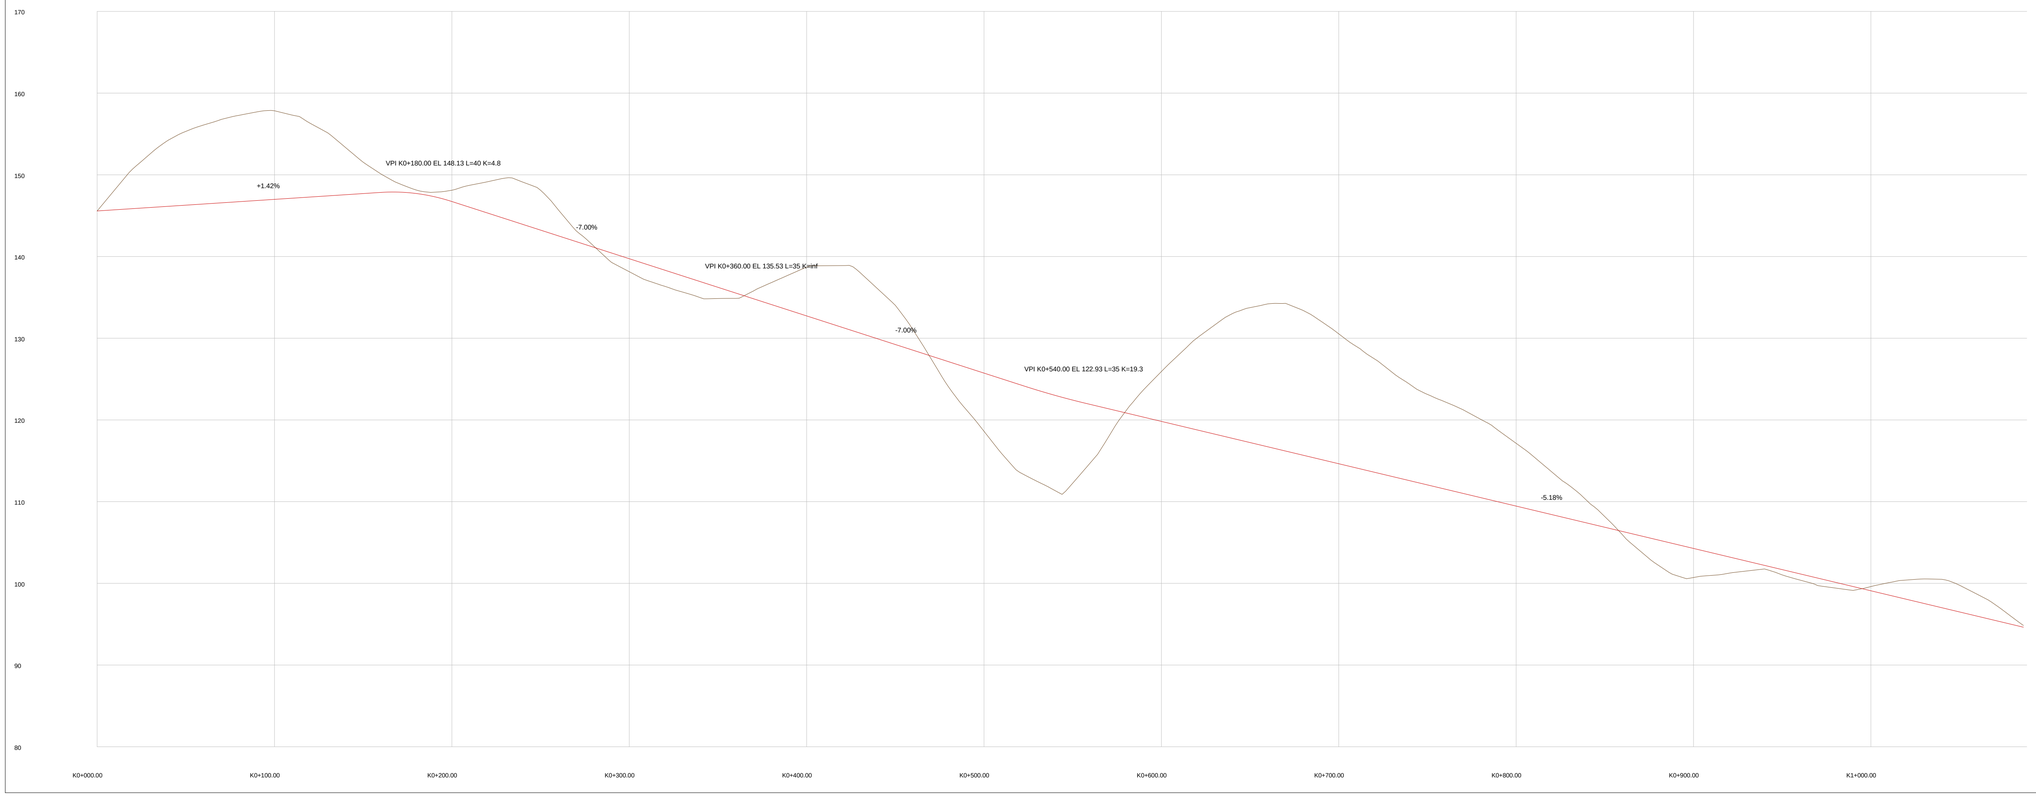

Demo access road (USGS 3DEP terrain, Palo Alto CA)

Std: JtgD20_2017

Design speed: 40 km/h

Checks: 19/19 pass

Cut 127513 m3 Fill 22543 m3

Audit log head:

991ba5ad897e897f4d2a7c7e849d86
e150effbe5d2670d50839e9b4b383aa69

Prepared by: civil-mcp agent tools

Engineer in responsible charge: REVIEWER-PLACEHOLDER

PRELIMINARY

NOT FOR CONSTRUCTION

Not reviewed or sealed by

a licensed engineer.

ENGINEER SEAL / SIGNATURE