

平面图 PLAN 1:4000 等高线 1 m（计曲线 5 m） N↑

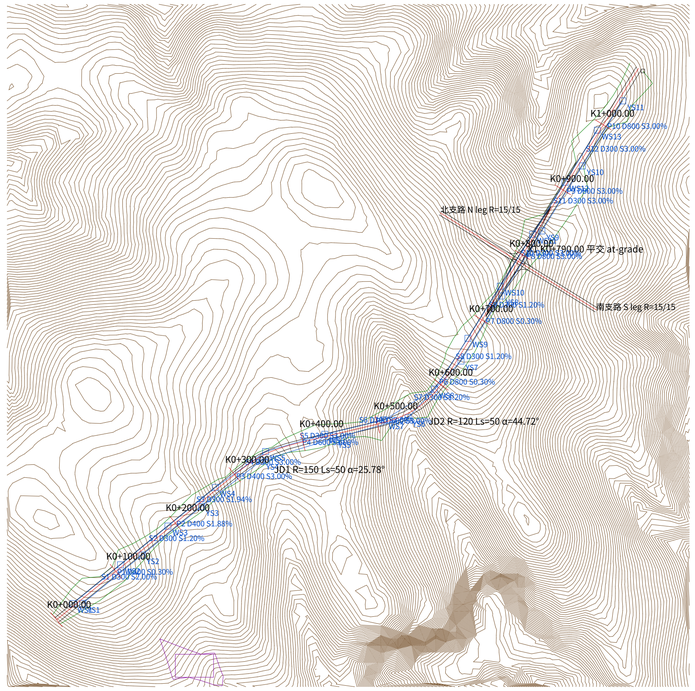

纵断面图 PROFILE H 1:1750 V 1:391（地面线棕色，设计线红色）

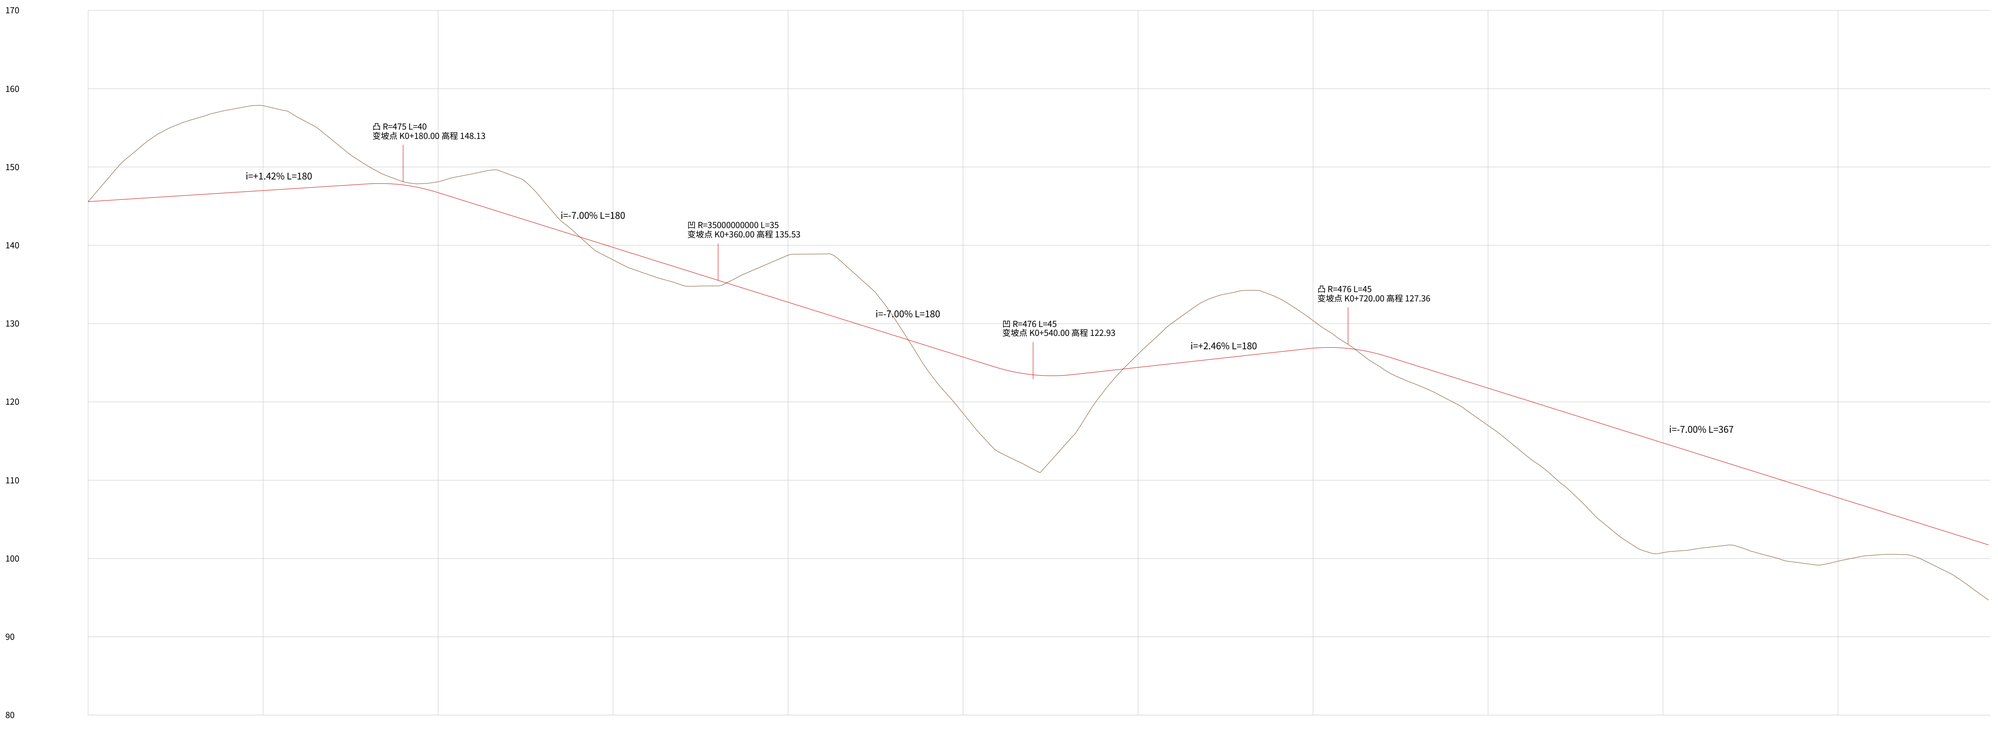

演示道路 Demo access road (USGS 3DEP, Palo Alto CA)

图名 Sheet: 平纵面图 Plan & Profile

图号 1/10

规范 Std: JtgD20_2017

设计速度 Design speed: 40 km/h

检查 Checks: 201/201 通过 pass

审计日志 Audit log head:

26a1feaa410e80a4d763e2d5cd522d40
d9ad812cbce097e0b523a305b4408358

编制 Prepared by: civil-mcp agent tools

负责工程师 Engineer in responsible charge:

REVIEWER-PLACEHOLDER

初步设计 PRELIMINARY

不得用于施工


NOT FOR CONSTRUCTION

未经注册工程师审核盖章

Not reviewed or sealed by a licensed engineer.


注册工程师签章 ENGINEER SEAL / SIGNATURE

桩号 K0+000.00

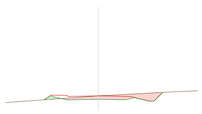


设计 145.58 地面 145.58 挖 7.0 m² 填 0.5 m²
横坡 左 -2.00% 右 -2.00% 坡脚/坡顶 左 6.4 右 7.1 m

桩号 K0+020.00

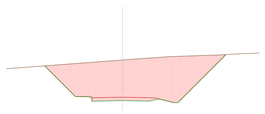


设计 145.86 地面 150.71 挖 98.2 m² 填 0.0 m²
横坡 左 -2.00% 右 -2.00% 坡脚/坡顶 左 13.5 右 10.2 m

桩号 K0+040.00

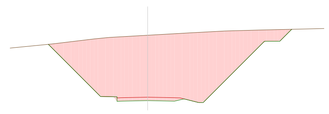


设计 146.14 地面 154.23 挖 187.0 m² 填 0.0 m²
横坡 左 -2.00% 右 -2.00% 坡脚/坡顶 左 18.8 右 13.0 m

桩号 K0+060.00

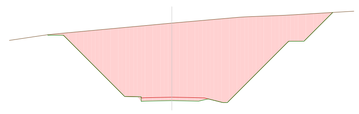


设计 146.43 地面 156.10 挖 244.5 m² 填 0.0 m²
横坡 左 -2.00% 右 -2.00% 坡脚/坡顶 左 21.0 右 16.2 m

桩号 K0+080.00

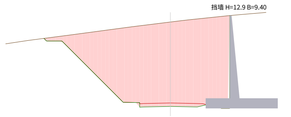


设计 146.71 地面 157.28 挖 196.3 m² 填 0.0 m²
横坡 左 -2.00% 右 -2.00% 坡脚/坡顶 左 7.8 右 16.5 m

桩号 K0+100.00

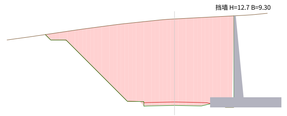


设计 147.00 地面 157.84 挖 204.0 m² 填 0.0 m²
横坡 左 -2.00% 右 -2.00% 坡脚/坡顶 左 7.8 右 16.9 m

桩号 K0+120.00

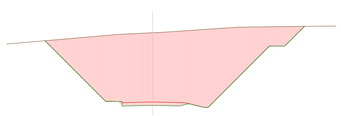


设计 147.28 地面 156.32 挖 220.7 m² 填 0.0 m²
横坡 左 -2.00% 右 -2.00% 坡脚/坡顶 左 19.8 右 14.1 m

桩号 K0+140.00

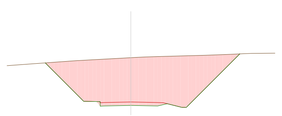


设计 147.56 地面 153.35 挖 119.7 m² 填 0.0 m²
横坡 左 -2.00% 右 -2.00% 坡脚/坡顶 左 14.2 右 11.2 m

桩号 K0+160.00

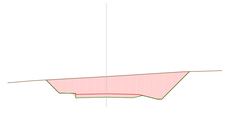


设计 147.85 地面 150.10 挖 43.8 m² 填 0.0 m²
横坡 左 -2.00% 右 -2.00% 坡脚/坡顶 左 10.9 右 7.9 m

桩号 K0+180.00

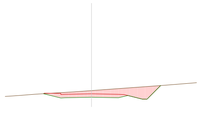


设计 147.71 地面 148.13 挖 13.8 m² 填 0.0 m²
横坡 左 -2.00% 右 -2.00% 坡脚/坡顶 左 9.0 右 6.3 m

桩号 K0+200.00

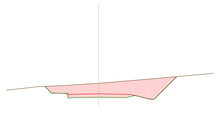

设计 146.73 地面 148.11 挖 29.0 m² 填 0.0 m²
横坡 左 -2.00% 右 -2.00% 坡脚/坡顶 左 10.2 右 7.0 m

桩号 K0+220.00

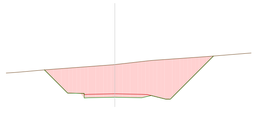

设计 145.33 地面 149.15 挖 77.5 m² 填 0.0 m²
横坡 左 -2.00% 右 -2.00% 坡脚/坡顶 左 12.9 右 9.2 m

演示道路 Demo access road (USGS 3DEP, Palo Alto CA)

图名 Sheet: 横断面图 Cross sections
图号 2/10
规范 Std: JtgD20_2017
设计速度 Design speed: 40 km/h
检查 Checks: 201/201 通过 pass
审计日志 Audit log head:
26a1feaa410e80a4d763e2d5cd522d40
d9ad812cbce097e0b523a305b4408358
编制 Prepared by: civil-mcp agent tools
负责工程师 Engineer in responsible charge:
REVIEWER-PLACEHOLDER

初步设计 PRELIMINARY

不得用于施工


NOT FOR CONSTRUCTION

未经注册工程师审核盖章
Not reviewed or sealed by a licensed engineer.

注册工程师签章 ENGINEER SEAL / SIGNATURE


横断面图 CROSS SECTIONS 1:400（红=挖方 cut，绿=填方 fill，绿线=路基设计线 datum）

桩号 K0+240.00

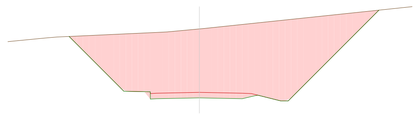


设计 143.93 地面 149.11 挖 111.0 m² 填 0.0 m²
横坡 左 -2.00% 右 -2.00% 坡脚/坡顶 左 14.7 右 10.6 m

桩号 K0+260.00

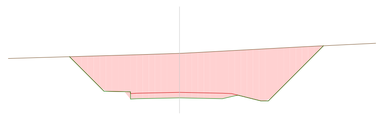


设计 142.53 地面 145.71 挖 62.4 m² 填 0.0 m²
横坡 左 -2.00% 右 -2.00% 坡脚/坡顶 左 11.8 右 9.0 m

桩号 K0+280.00

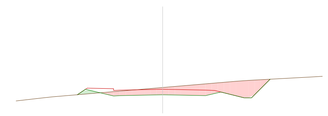


设计 141.13 地面 141.28 挖 9.9 m² 填 0.4 m²
横坡 左 -2.00% 右 -2.00% 坡脚/坡顶 左 8.8 右 7.0 m

桩号 K0+288.82

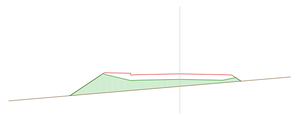


设计 140.51 地面 139.49 挖 0.0 m² 填 9.3 m²
横坡 左 -2.00% 右 -2.00% 坡脚/坡顶 左 5.0 右 9.0 m

桩号 K0+300.00

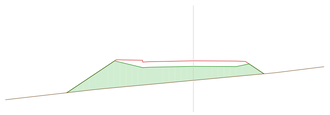


设计 139.73 地面 138.14 挖 0.0 m² 填 18.6 m²
横坡 左 -0.57% 右 -2.00% 坡脚/坡顶 左 5.8 右 10.3 m

桩号 K0+320.00

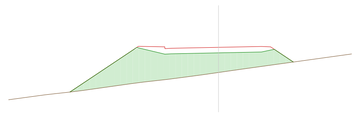


设计 138.33 地面 136.28 挖 0.0 m² 填 28.9 m²
横坡 左 +1.99% 右 -2.00% 坡脚/坡顶 左 6.1 右 12.1 m

桩号 K0+338.82

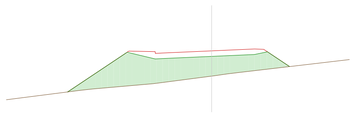


设计 137.01 地面 134.95 挖 0.0 m² 填 28.2 m²
横坡 左 +4.40% 右 -4.40% 坡脚/坡顶 左 6.4 右 11.8 m

桩号 K0+340.00

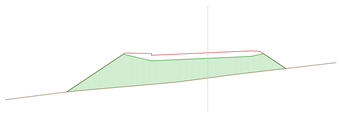


设计 136.93 地面 134.87 挖 0.0 m² 填 27.5 m²
横坡 左 +4.40% 右 -4.40% 坡脚/坡顶 左 6.4 右 11.5 m

桩号 K0+342.50

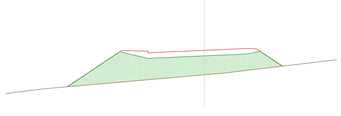


设计 136.76 地面 134.76 挖 0.0 m² 填 25.6 m²
横坡 左 +4.40% 右 -4.40% 坡脚/坡顶 左 6.4 右 11.2 m

桩号 K0+356.31

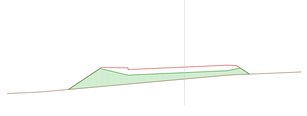


设计 135.79 地面 134.81 挖 0.0 m³ 填 9.6 m³
横坡 左 +4.40% 右 -4.40% 坡脚/坡顶 左 5.3 右 9.5 m

桩号 K0+360.00

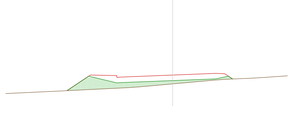

设计 135.53 地面 134.81 挖 0.0 m³ 填 5.3 m³
横坡 左 +3.93% 右 -3.93% 坡脚/坡顶 左 4.9 右 8.6 m

桩号 K0+377.50

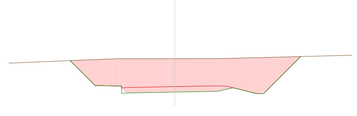

设计 134.31 地面 136.58 挖 42.8 m² 填 0.0 m²
横坡 左 +1.69% 右 -2.00% 坡脚/坡顶 左 10.3 右 8.5 m

演示道路 Demo access road (USGS 3DEP, Palo Alto CA)

图名 Sheet: 横断面图 Cross sections
图号 3/10
规范 Std: JtgD20_2017
设计速度 Design speed: 40 km/h
检查 Checks: 201/201 通过 pass
审计日志 Audit log head:
26a1feaa410e80a4d763e2d5cd522d40
d9ad812cbce097e0b523a305b4408358
编制 Prepared by: civil-mcp agent tools
负责工程师 Engineer in responsible charge:
REVIEWER-PLACEHOLDER

初步设计 PRELIMINARY

不得用于施工


NOT FOR CONSTRUCTION

未经注册工程师审核盖章
Not reviewed or sealed by a licensed engineer.

注册工程师签章 ENGINEER SEAL / SIGNATURE


横断面图 CROSS SECTIONS 1:250（红=挖方 cut，绿=填方 fill，绿线=路基设计线 datum）

桩号 K0+380.00

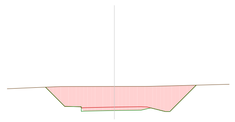


设计 134.13 地面 136.82 挖 50.9 m² 填 0.0 m²
横坡 左 +1.37% 右 -2.00% 坡脚/坡顶 左 10.7 右 9.0 m

桩号 K0+400.00

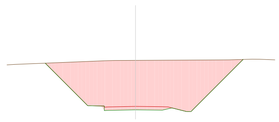


设计 132.73 地面 138.74 挖 124.8 m² 填 0.0 m²
横坡 左 -1.19% 右 -2.00% 坡脚/坡顶 左 14.1 右 11.8 m

桩号 K0+406.31

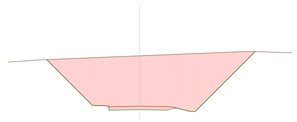


设计 132.29 地面 138.86 挖 142.3 m² 填 0.0 m²
横坡 左 -2.00% 右 -2.00% 坡脚/坡顶 左 15.1 右 12.2 m

桩号 K0+420.00

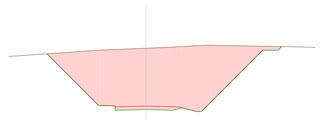


设计 131.33 地面 138.89 挖 169.4 m² 填 0.0 m²
横坡 左 -2.00% 右 -2.00% 坡脚/坡顶 左 17.7 右 12.9 m

桩号 K0+440.00

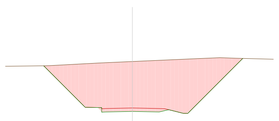


设计 129.93 地面 136.00 挖 128.2 m² 填 0.0 m²
横坡 左 -2.00% 右 -2.00% 坡脚/坡顶 左 14.4 右 11.6 m

桩号 K0+460.00

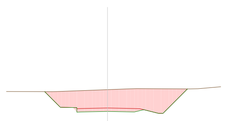


设计 128.53 地面 130.93 挖 44.6 m² 填 0.0 m²
横坡 左 -2.00% 右 -2.00% 坡脚/坡顶 左 10.4 右 8.2 m

桩号 K0+480.00

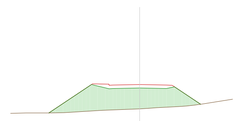


设计 127.13 地面 123.95 挖 0.0 m² 填 44.2 m²
横坡 左 -2.00% 右 -2.00% 坡脚/坡顶 左 8.0 右 11.9 m

桩号 K0+488.04

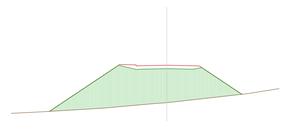


设计 126.57 地面 121.68 挖 0.0 m² 填 84.2 m²
横坡 左 -2.00% 右 -2.00% 坡脚/坡顶 左 9.8 右 15.3 m

桩号 K0+500.00

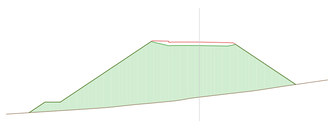


设计 125.73 地面 118.54 挖 0.0 m² 填 159.9 m²
横坡 左 -2.00% 右 +0.03% 坡脚/坡顶 左 12.6 右 22.2 m

桩号 K0+517.50

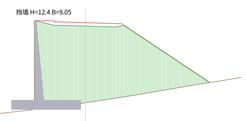


设计 124.51 地面 114.05 挖 0.0 m³ 填 171.4 m³
横坡 左 -3.01% 右 +3.01% 坡脚/坡顶 左 16.2 右 6.7 m

桩号 K0+520.00

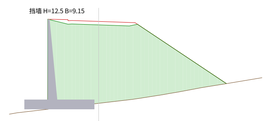

设计 124.34 地面 113.65 挖 0.0 m³ 填 178.8 m³
横坡 左 -3.43% 右 +3.43% 坡脚/坡顶 左 16.7 右 6.7 m

桩号 K0+538.04

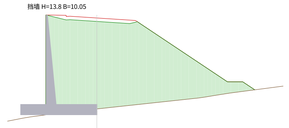

设计 123.51 地面 111.64 挖 0.0 m² 填 215.8 m²
横坡 左 -6.50% 右 +6.50% 坡脚/坡顶 左 20.6 右 6.7 m

演示道路 Demo access road (USGS 3DEP, Palo Alto CA)

图名 Sheet: 横断面图 Cross sections
图号 4/10
规范 Std: JtgD20_2017
设计速度 Design speed: 40 km/h
检查 Checks: 201/201 通过 pass
审计日志 Audit log head:
26a1feaa410e80a4d763e2d5cd522d40
d9ad812cbce097e0b523a305b4408358
编制 Prepared by: civil-mcp agent tools
负责工程师 Engineer in responsible charge:
REVIEWER-PLACEHOLDER

初步设计 PRELIMINARY

不得用于施工


NOT FOR CONSTRUCTION

未经注册工程师审核盖章
Not reviewed or sealed by a licensed engineer.

注册工程师签章 ENGINEER SEAL / SIGNATURE


横断面图 CROSS SECTIONS 1:400（红=挖方 cut，绿=填方 fill，绿线=路基设计线 datum）

桩号 K0+540.00

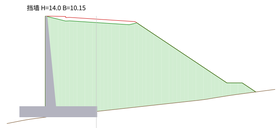


设计 123.46 地面 111.40 挖 0.0 m² 填 220.5 m²
横坡 左 -6.50% 右 +6.50% 坡脚/坡顶 左 20.8 右 6.7 m

桩号 K0+560.00

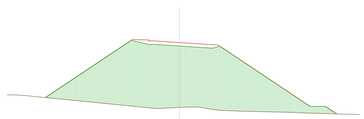


设计 123.43 地面 114.96 挖 0.0 m² 填 199.3 m²
横坡 左 -6.50% 右 +6.50% 坡脚/坡顶 左 20.5 右 17.5 m

桩号 K0+562.50

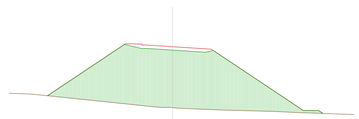


设计 123.49 地面 115.50 挖 0.0 m² 填 174.1 m²
横坡 左 -6.50% 右 +6.50% 坡脚/坡顶 左 19.6 右 16.3 m

桩号 K0+580.00

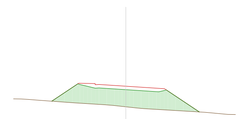


设计 123.92 地面 121.23 挖 0.0 m² 填 36.1 m²
横坡 左 -6.50% 右 +6.50% 坡脚/坡顶 左 9.6 右 9.7 m

桩号 K0+581.69

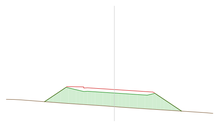


设计 123.96 地面 121.72 挖 0.0 m² 填 27.7 m²
横坡 左 -6.50% 右 +6.50% 坡脚/坡顶 左 8.8 右 9.1 m

桩号 K0+600.00

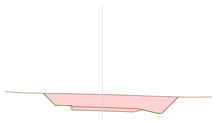


设计 124.41 地面 126.10 挖 31.7 m² 填 0.0 m²
横坡 左 -3.39% 右 +3.39% 坡脚/坡顶 左 9.9 右 7.7 m

桩号 K0+620.00

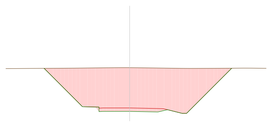


设计 124.90 地面 130.16 挖 106.0 m² 填 0.0 m²
横坡 左 -2.00% 右 -0.01% 坡脚/坡顶 左 13.3 右 11.2 m

桩号 K0+631.69

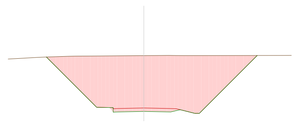


设计 125.19 地面 132.03 挖 147.5 m² 填 0.0 m²
横坡 左 -2.00% 右 -2.00% 坡脚/坡顶 左 14.8 右 12.7 m

桩号 K0+640.00

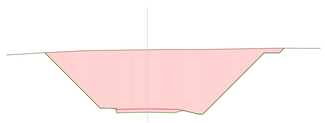


设计 125.39 地面 133.11 挖 173.6 m² 填 0.0 m²
横坡 左 -2.00% 右 -2.00% 坡脚/坡顶 左 17.9 右 13.4 m

桩号 K0+660.00

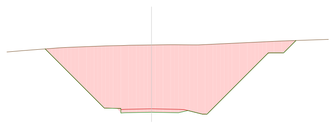


设计 125.89 地面 134.22 挖 195.1 m² 填 0.0 m²
横坡 左 -2.00% 右 -2.00% 坡脚/坡顶 左 18.9 右 13.9 m

桩号 K0+680.00

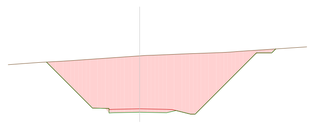

设计 126.38 地面 133.29 挖 150.7 m² 填 0.0 m²
横坡 左 -2.00% 右 -2.00% 坡脚/坡顶 左 17.8 右 12.2 m

桩号 K0+697.50

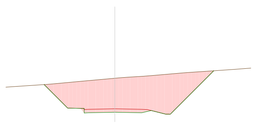

设计 126.81 地面 130.80 挖 79.1 m² 填 0.0 m²
横坡 左 -2.00% 右 -2.00% 坡脚/坡顶 左 12.9 右 9.2 m

演示道路 Demo access road (USGS 3DEP, Palo Alto CA)

图名 Sheet: 横断面图 Cross sections
图号 5/10
规范 Std: JtgD20_2017
设计速度 Design speed: 40 km/h
检查 Checks: 201/201 通过 pass
审计日志 Audit log head:
26a1feaa410e80a4d763e2d5cd522d40
d9ad812cbce097e0b523a305b4408358
编制 Prepared by: civil-mcp agent tools
负责工程师 Engineer in responsible charge:
REVIEWER-PLACEHOLDER

初步设计 PRELIMINARY

不得用于施工


NOT FOR CONSTRUCTION

未经注册工程师审核盖章
Not reviewed or sealed by a licensed engineer.

注册工程师签章 ENGINEER SEAL / SIGNATURE


横断面图 CROSS SECTIONS 1:400（红=挖方 cut，绿=填方 fill，绿线=路基设计线 datum）

桩号 K0+700.00

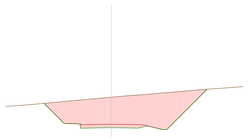


设计 126.86 地面 130.38 挖 69.4 m² 填 0.0 m²
横坡 左 -2.00% 右 -2.00% 坡脚/坡顶 左 12.5 右 8.8 m

桩号 K0+720.00

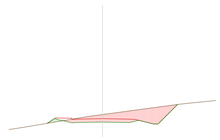


设计 126.83 地面 127.36 挖 16.9 m² 填 0.5 m²
横坡 左 -2.00% 右 -2.00% 坡脚/坡顶 左 9.8 右 7.2 m

桩号 K0+740.00

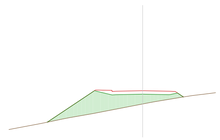


设计 125.96 地面 124.22 挖 0.0 m² 填 25.2 m²
横坡 左 -2.00% 右 -2.00% 坡脚/坡顶 左 5.3 右 12.5 m

桩号 K0+742.50

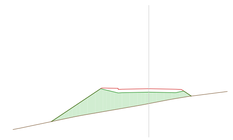


设计 125.79 地面 123.84 挖 0.0 m² 填 28.1 m²
横坡 左 -2.00% 右 -2.00% 坡脚/坡顶 左 5.5 右 12.7 m

桩号 K0+760.00

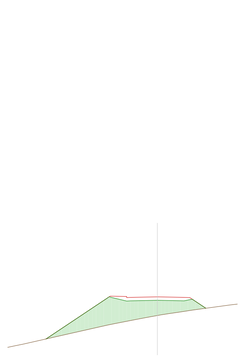


设计 124.56 地面 122.12 挖 0.0 m² 填 40.1 m²
横坡 左 -2.00% 右 -2.00% 坡脚/坡顶 左 6.3 右 14.5 m

桩号 K0+780.00

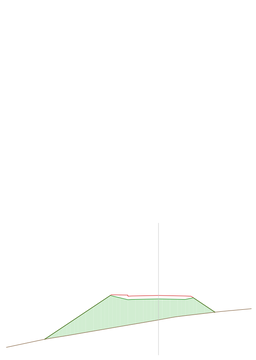


设计 123.16 地面 119.97 挖 0.0 m² 填 53.1 m²
横坡 左 -2.00% 右 -2.00% 坡脚/坡顶 左 7.4 右 14.9 m

桩号 K0+800.00

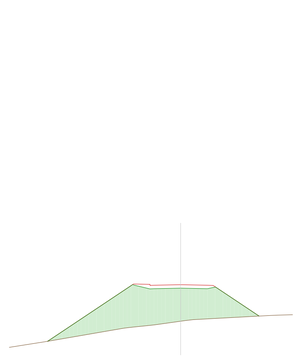


设计 121.76 地面 117.00 挖 0.0 m² 填 90.7 m²
横坡 左 -2.00% 右 -2.00% 坡脚/坡顶 左 10.2 右 17.4 m

桩号 K0+820.00

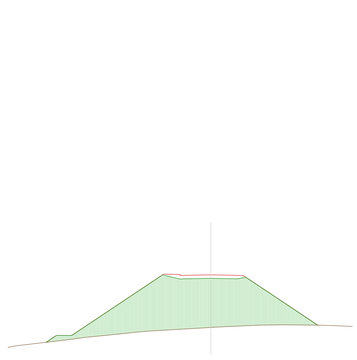


设计 120.36 地面 113.49 挖 0.0 m² 填 146.8 m²
横坡 左 -2.00% 右 -2.00% 坡脚/坡顶 左 14.0 右 21.5 m

桩号 K0+840.00

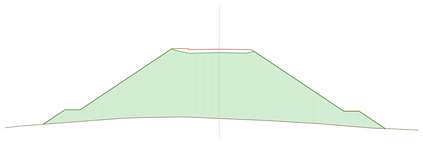


设计 118.96 地面 109.91 挖 0.0 m² 填 230.2 m²
横坡 左 -2.00% 右 -2.00% 坡脚/坡顶 左 21.7 右 23.0 m

桩号 K0+860.00

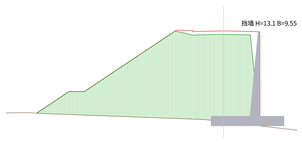


设计 117.56 地面 105.71 挖 0.0 m³ 填 216.7 m³
横坡 左 -2.00% 右 -2.00% 坡脚/坡顶 左 4.8 右 24.4 m

桩号 K0+880.00

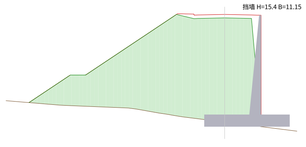

设计 116.16 地面 102.10 挖 0.0 m³ 填 260.0 m³
横坡 左 -2.00% 右 -2.00% 坡脚/坡顶 左 4.8 右 25.6 m

桩号 K0+900.00

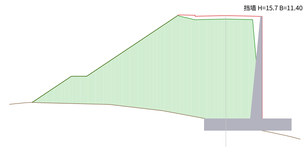

设计 114.76 地面 100.75 挖 0.0 m² 填 251.0 m²
横坡 左 -2.00% 右 -2.00% 坡脚/坡顶 左 4.8 右 25.3 m

演示道路 Demo access road (USGS 3DEP, Palo Alto CA)

图名 Sheet: 横断面图 Cross sections
图号 6/10
规范 Std: JtgD20_2017
设计速度 Design speed: 40 km/h
检查 Checks: 201/201 通过 pass
审计日志 Audit log head:
26a1feaa410e80a4d763e2d5cd522d40
d9ad812cbce097e0b523a305b4408358
编制 Prepared by: civil-mcp agent tools
负责工程师 Engineer in responsible charge:
REVIEWER-PLACEHOLDER

初步设计 PRELIMINARY

不得用于施工


NOT FOR CONSTRUCTION

未经注册工程师审核盖章
Not reviewed or sealed by a licensed engineer.

注册工程师签章 ENGINEER SEAL / SIGNATURE


横断面图 CROSS SECTIONS 1:400（红=挖方 cut，绿=填方 fill，绿线=路基设计线 datum）

桩号 K0+920.00

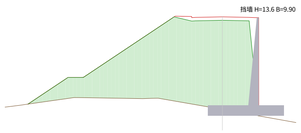


设计 113.36 地面 101.28 挖 0.0 m² 填 211.3 m²
横坡 左 -2.00% 右 -2.00% 坡脚/坡顶 左 4.8 右 25.4 m

桩号 K0+940.00

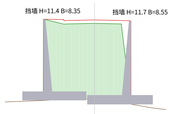


设计 111.96 地面 101.71 挖 0.0 m² 填 108.1 m²
横坡 左 -2.00% 右 -2.00% 坡脚/坡顶 左 4.8 右 6.7 m

桩号 K0+960.00

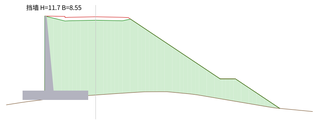


设计 110.56 地面 100.35 挖 0.0 m² 填 193.2 m²
横坡 左 -2.00% 右 -2.00% 坡脚/坡顶 左 24.0 右 6.7 m

桩号 K0+980.00

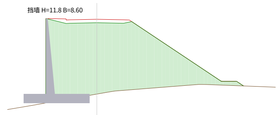


设计 109.16 地面 99.40 挖 0.0 m² 填 162.0 m²
横坡 左 -2.00% 右 -2.00% 坡脚/坡顶 左 19.2 右 6.7 m

桩号 K1+000.00

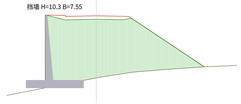


设计 107.76 地面 99.66 挖 0.0 m² 填 122.5 m²
横坡 左 -2.00% 右 -2.00% 坡脚/坡顶 左 14.1 右 6.7 m

桩号 K1+020.00

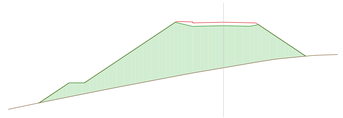


设计 106.36 地面 100.42 挖 0.0 m² 填 133.2 m²
横坡 左 -2.00% 右 -2.00% 坡脚/坡顶 左 10.7 右 24.1 m

桩号 K1+040.00

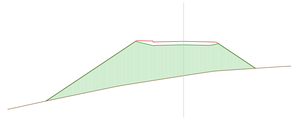


设计 104.96 地面 100.48 挖 0.0 m² 填 85.5 m²
横坡 左 -2.00% 右 -2.00% 坡脚/坡顶 左 9.4 右 18.0 m

桩号 K1+060.00

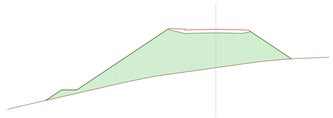


设计 103.56 地面 98.56 挖 0.0 m² 填 100.5 m²
横坡 左 -2.00% 右 -2.00% 坡脚/坡顶 左 9.9 右 22.2 m

桩号 K1+080.00

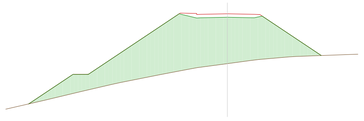

设计 102.16 地面 95.65 挖 0.0 m² 填 156.1 m²
横坡 左 -2.00% 右 -2.00% 坡脚/坡顶 左 12.3 右 25.9 m

桩号 K1+087.02

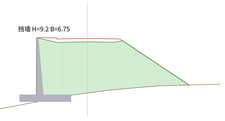

设计 101.67 地面 94.53 挖 0.0 m² 填 104.5 m²
横坡 左 -2.00% 右 -2.00% 坡脚/坡顶 左 13.2 右 6.7 m

演示道路 Demo access road (USGS 3DEP, Palo Alto CA)

图名 Sheet: 横断面图 Cross sections
图号 7/10
规范 Std: JtgD20_2017
设计速度 Design speed: 40 km/h
检查 Checks: 201/201 通过 pass
审计日志 Audit log head:
26a1feaa410e80a4d763e2d5cd522d40
d9ad812cbce097e0b523a305b4408358
编制 Prepared by: civil-mcp agent tools
负责工程师 Engineer in responsible charge:
REVIEWER-PLACEHOLDER

初步设计 PRELIMINARY

不得用于施工

NOT FOR CONSTRUCTION


未经注册工程师审核盖章
Not reviewed or sealed by a licensed engineer.

注册工程师签章 ENGINEER SEAL / SIGNATURE

横断面图 CROSS SECTIONS 1:400（红=挖方 cut，绿=填方 fill，绿线=路基设计线 datum）

管道纵断面 PIPE PROFILE — 雨水 Storm H 1:1636 V 1:101

青=水力坡降线 HGL，红=能量线 EGL，棕=井顶 rim；方法 FHWA HEC-22 approximate method: outfall HGL = max(tailwater, invert + (dc+D)/2); full flow: HGL_up = HGL_dn + Sf · L, Sf = (Qn/(A R^(2/3)))²; partial flow: normal depth; structure: E = EGL_out + K · Vo²/2g, K by deflection (0°0.15, 22.5°0.45, 45°0.75, 60°0.85, 90°1.0; start structure 0.5). Coefficients transcribed — verify against the HEC-22 edition in use.

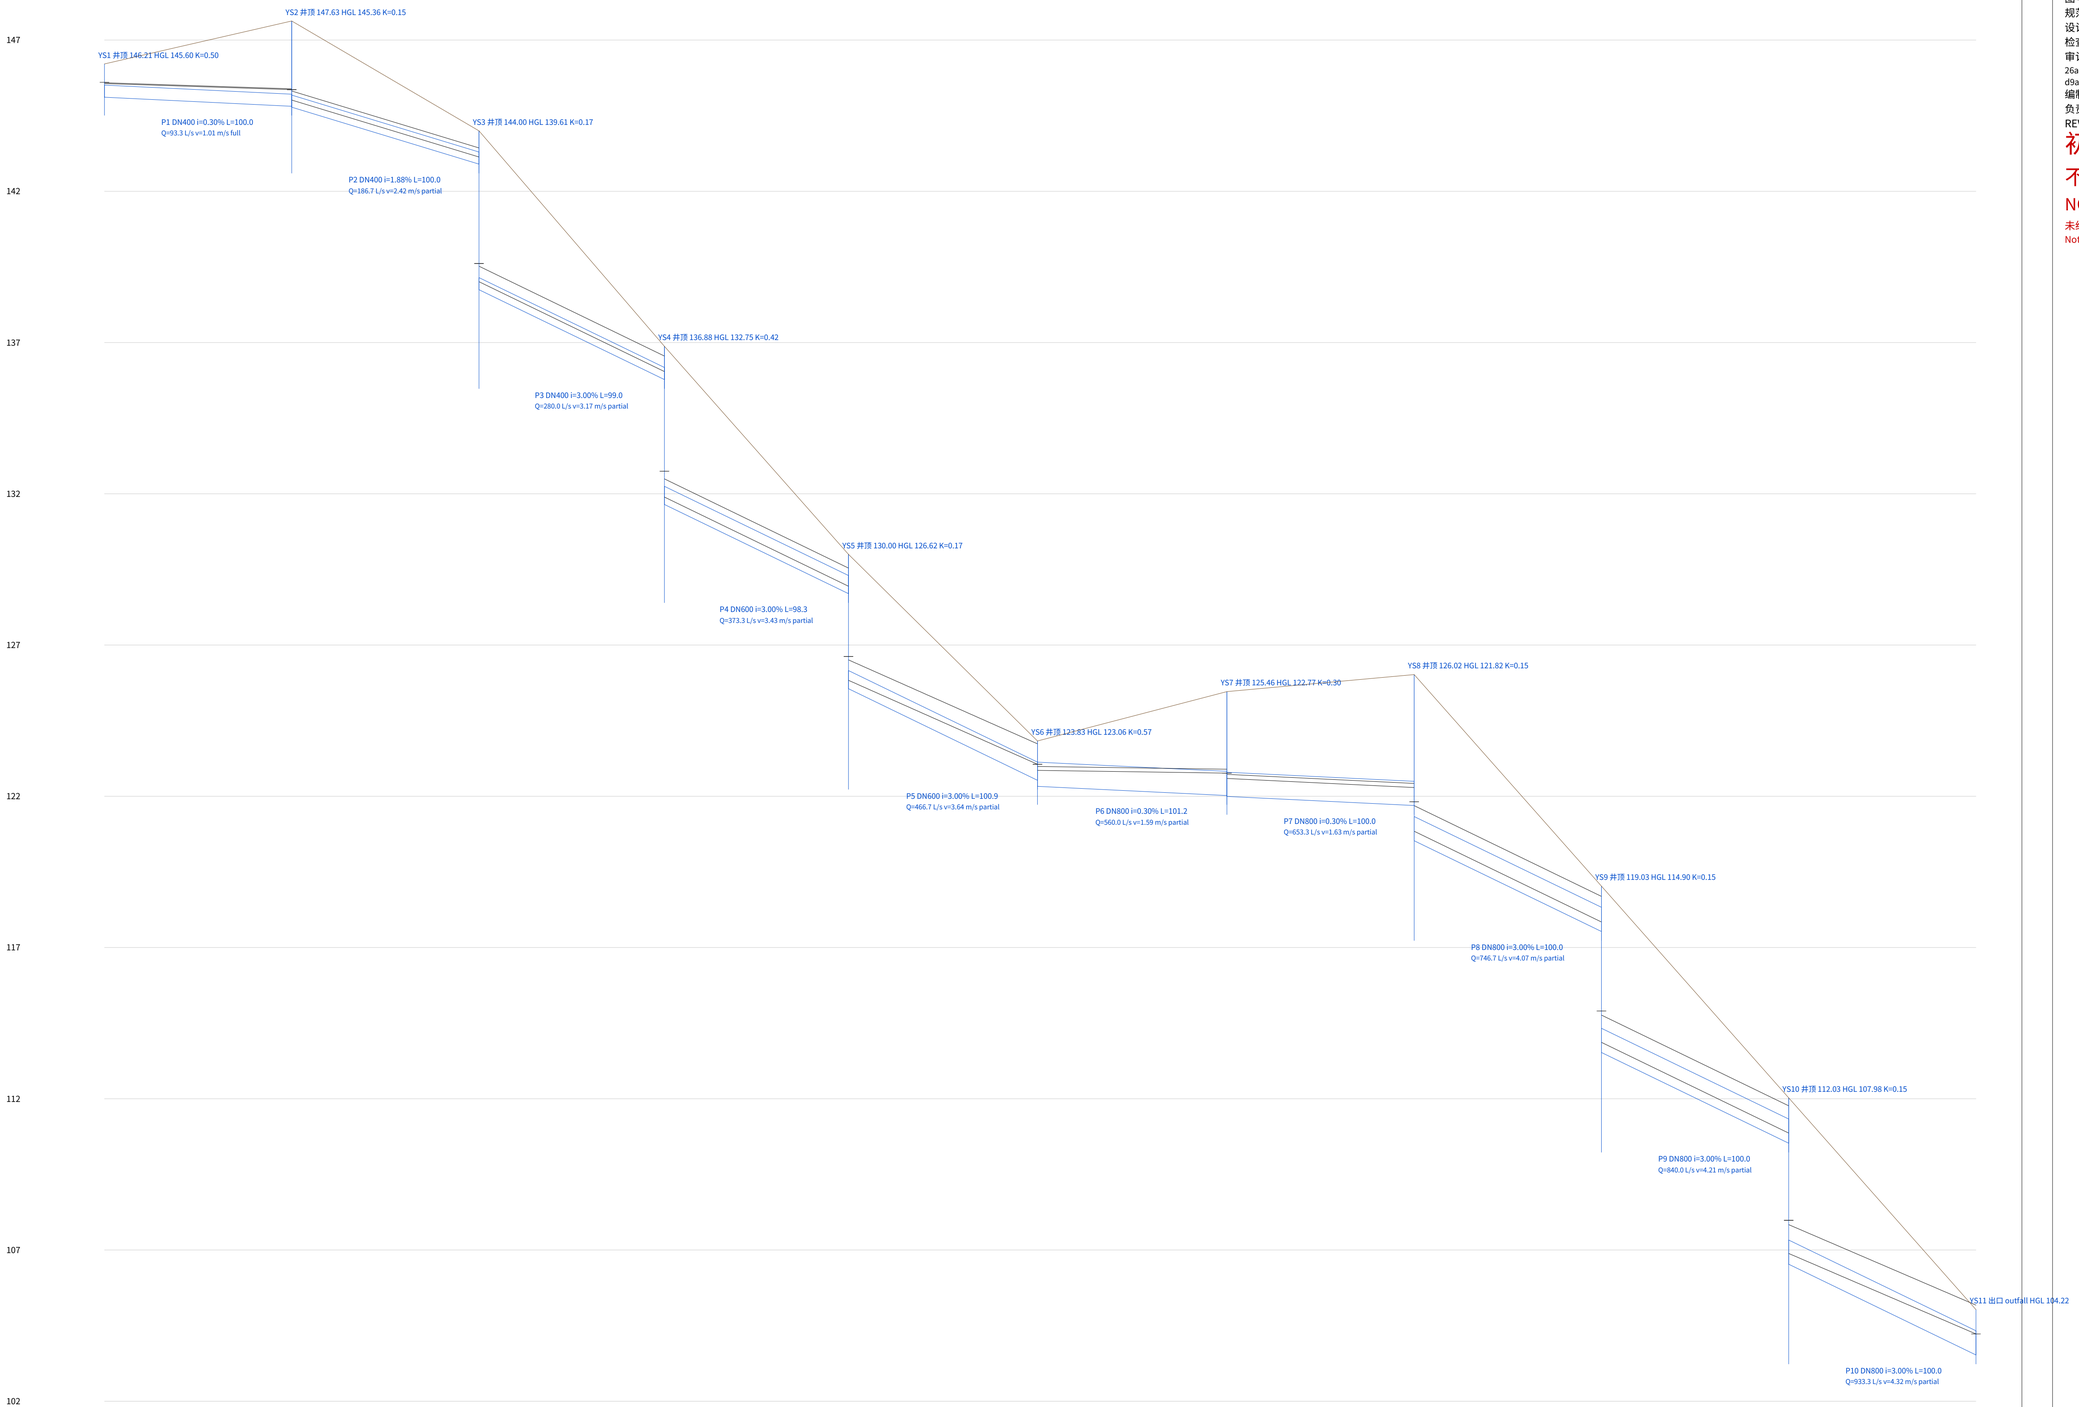

P-SURCH 提示 advisory pipe P1 Pipe flows full (surcharged): 0.150 vs max 0.000 m

演示道路 Demo access road (USGS 3DEP, Palo Alto CA)

图名 Sheet: 管道纵断面 Pipe profile 雨水 Storm
图号 8/10
规范 Std: JtgD20_2017
设计速度 Design speed: 40 km/h
检查 Checks: 201/201 通过 pass
审计日志 Audit log head:
26a1feaa410e80a4d763e2d5cd522d40
d9ad812cbce097e0b523a305b4408358
编制 Prepared by: civil-mcp agent tools
负责工程师 Engineer in responsible charge:
REVIEWER-PLACEHOLDER

初步设计 PRELIMINARY

不得用于施工


NOT FOR CONSTRUCTION

未经注册工程师审核盖章
Not reviewed or sealed by a licensed engineer.

注册工程师签章 ENGINEER SEAL / SIGNATURE

管道纵断面 PIPE PROFILE — 污水 Sanitary H 1:1567 V 1:93

青=水力坡降线 HGL，红=能量线 EGL，棕=井顶 rim；方法 FHWA HEC-22 approximate method: outfall HGL = max(tailwater, invert + (dc+D)/2); full flow: HGL_up = HGL_dn + Sf · L, Sf = (Qn/(A R^(2/3)))²; partial flow: normal depth; structure: E = EGL_out + K · Vo²/2g, K by deflection (0°0.15, 22.5°0.45, 45°0.75, 60°0.85, 90°1.0; start structure 0.5). Coefficients transcribed — verify against the HEC-22 edition in use.

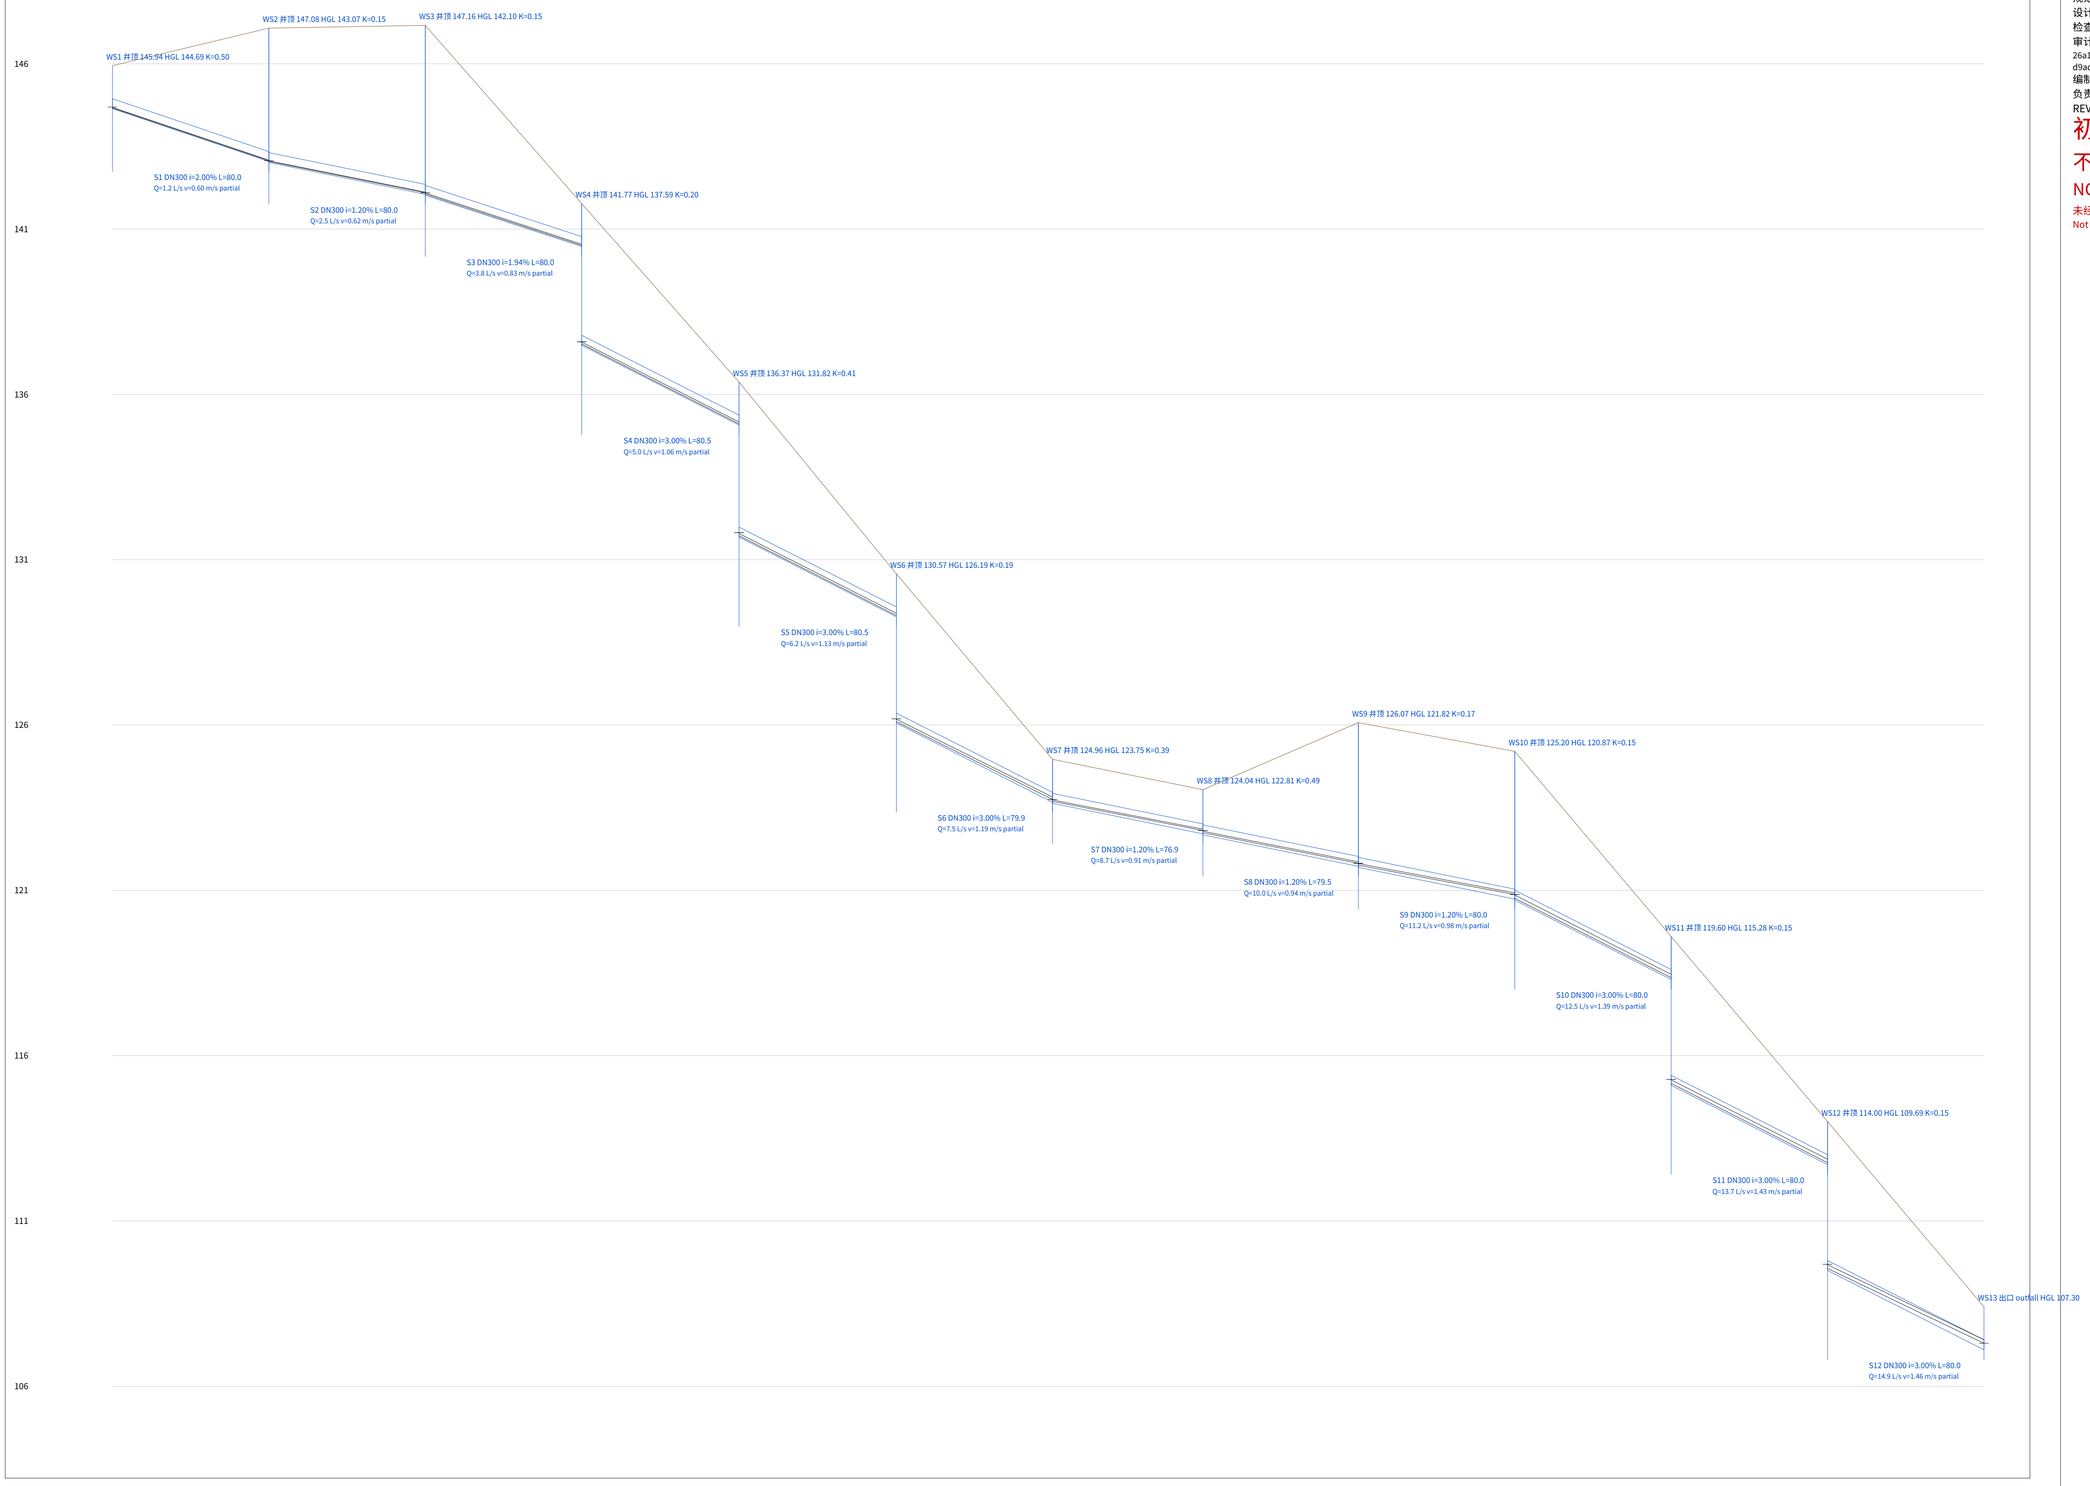

演示道路 Demo access road (USGS 3DEP, Palo Alto CA)

图名 Sheet: 管道纵断面 Pipe profile 污水 Sanitary

图号 9/10

规范 Std: JtgD20_2017

设计速度 Design speed: 40 km/h

检查 Checks: 201/201 通过 pass

审计日志 Audit log head:

26a1feaa410e80a4d763e2d5cd522d40

d9ad812cbce097e0b523a305b4408358

编制 Prepared by: civil-mcp agent tools

负责工程师 Engineer in responsible charge:

REVIEWER-PLACEHOLDER

初步设计 PRELIMINARY

不得用于施工


NOT FOR CONSTRUCTION

未经注册工程师审核盖章

Not reviewed or sealed by a licensed engineer.

注册工程师签章 ENGINEER SEAL / SIGNATURE

土方调配图 MASS HAUL (m³) 挖方系数 cut factor 0.90 终点累计 -17447 m³

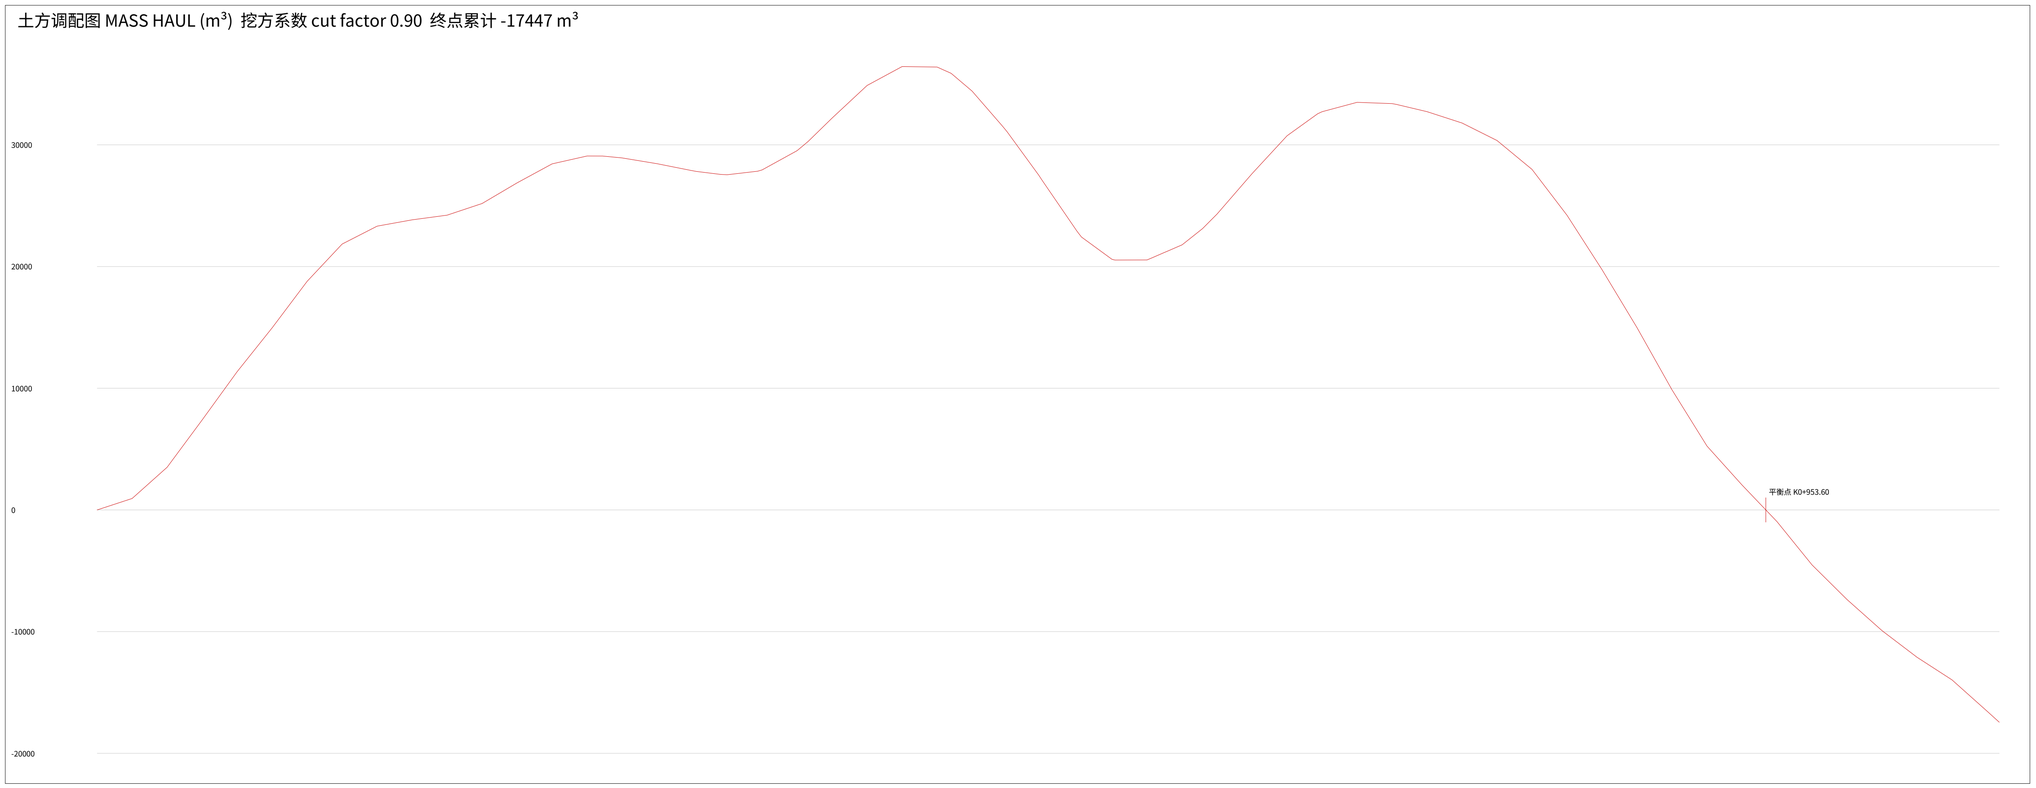

桩号范围 Station	挖方 Cut m³	填方 Fill m³	沥青面层 AC m³	水稳基层 Base m³	底基层 Subbase m³
K0+000.00–K0+100.00	16630	5	37.5	150.0	150.0
K0+100.00–K0+200.00	10290	0	37.5	150.0	150.0
K0+200.00–K0+300.00	5450	202	37.5	150.2	150.2
K0+300.00–K0+400.00	2250	1428	39.5	157.9	157.9
K0+400.00–K0+500.00	8126	2418	37.6	150.3	150.3
K0+500.00–K0+600.00	291	14137	40.8	163.1	163.1
K0+600.00–K0+700.00	13535	0	37.9	151.6	151.6
K0+700.00–K0+800.00	1032	3296	37.5	150.0	150.0
K0+800.00–K0+900.00	0	20490	37.5	150.0	150.0
K0+900.00–K1+000.00	0	17227	37.5	150.0	150.0
K1+000.00–K1+100.00	0	10086	32.6	130.5	130.5
合计 Total	57602	69289	413.4	1653.6	1653.6

管道材料表 Pipe schedule

钢筋混凝土管 RCP DN400: 299.0 m
钢筋混凝土管 RCP DN600: 199.2 m
钢筋混凝土管 RCP DN800: 501.2 m
检查井 Structures: 11

管道材料表 Pipe schedule

HDPE 双壁波纹管 DN300: 957.3 m
检查井 Structures: 13

场平 Grading yard: 挖 2475 m³ 填 2242 m³ (方格网 0.25 m)

演示道路 Demo access road (USGS 3DEP, Palo Alto CA)

图名 Sheet: 土方调配及工程量 Mass haul & quantities
图号 10/10
规范 Std: JtgD20_2017
设计速度 Design speed: 40 km/h
检查 Checks: 201/201 通过 pass
审计日志 Audit log head:
26a1feaa410e80a4d763e2d5cd522d40
d9ad812cbce097e0b523a305b4408358
编制 Prepared by: civil-mcp agent tools
负责工程师 Engineer in responsible charge:
REVIEWER-PLACEHOLDER

初步设计 PRELIMINARY

不得用于施工

NOT FOR CONSTRUCTION

未经注册工程师审核盖章
Not reviewed or sealed by a licensed engineer.

注册工程师签章 ENGINEER SEAL / SIGNATURE